


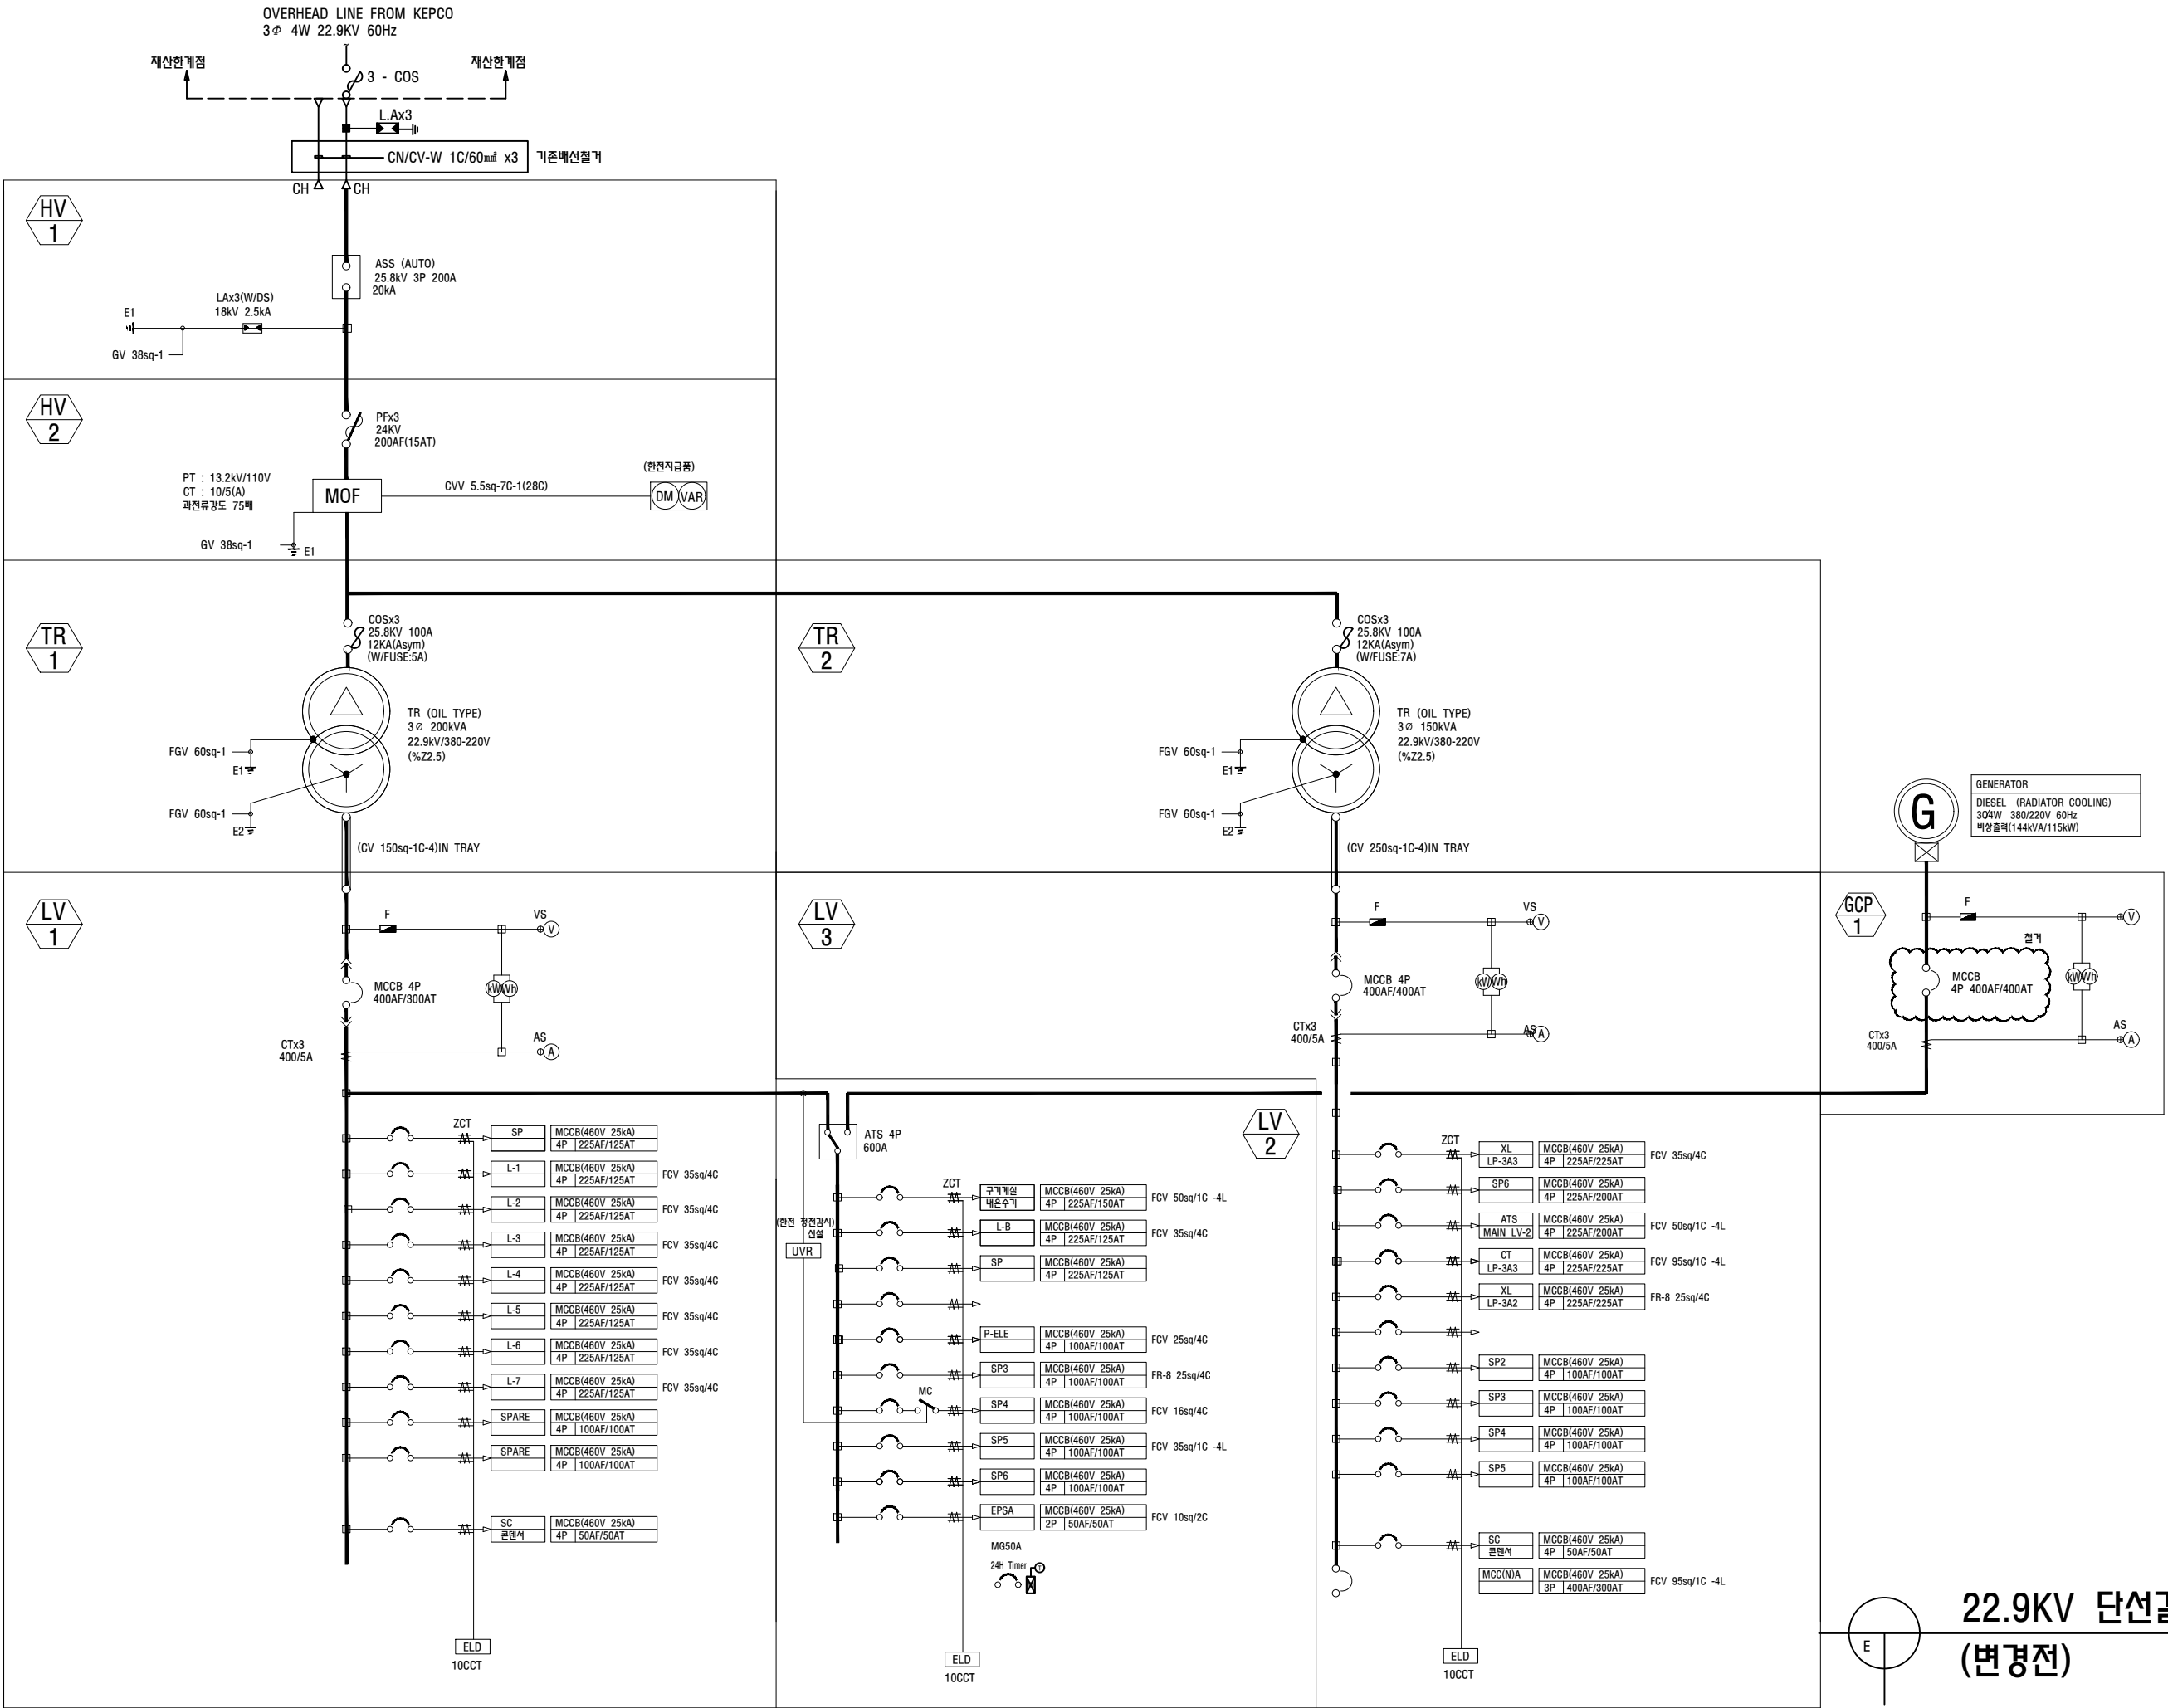


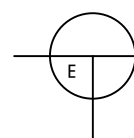

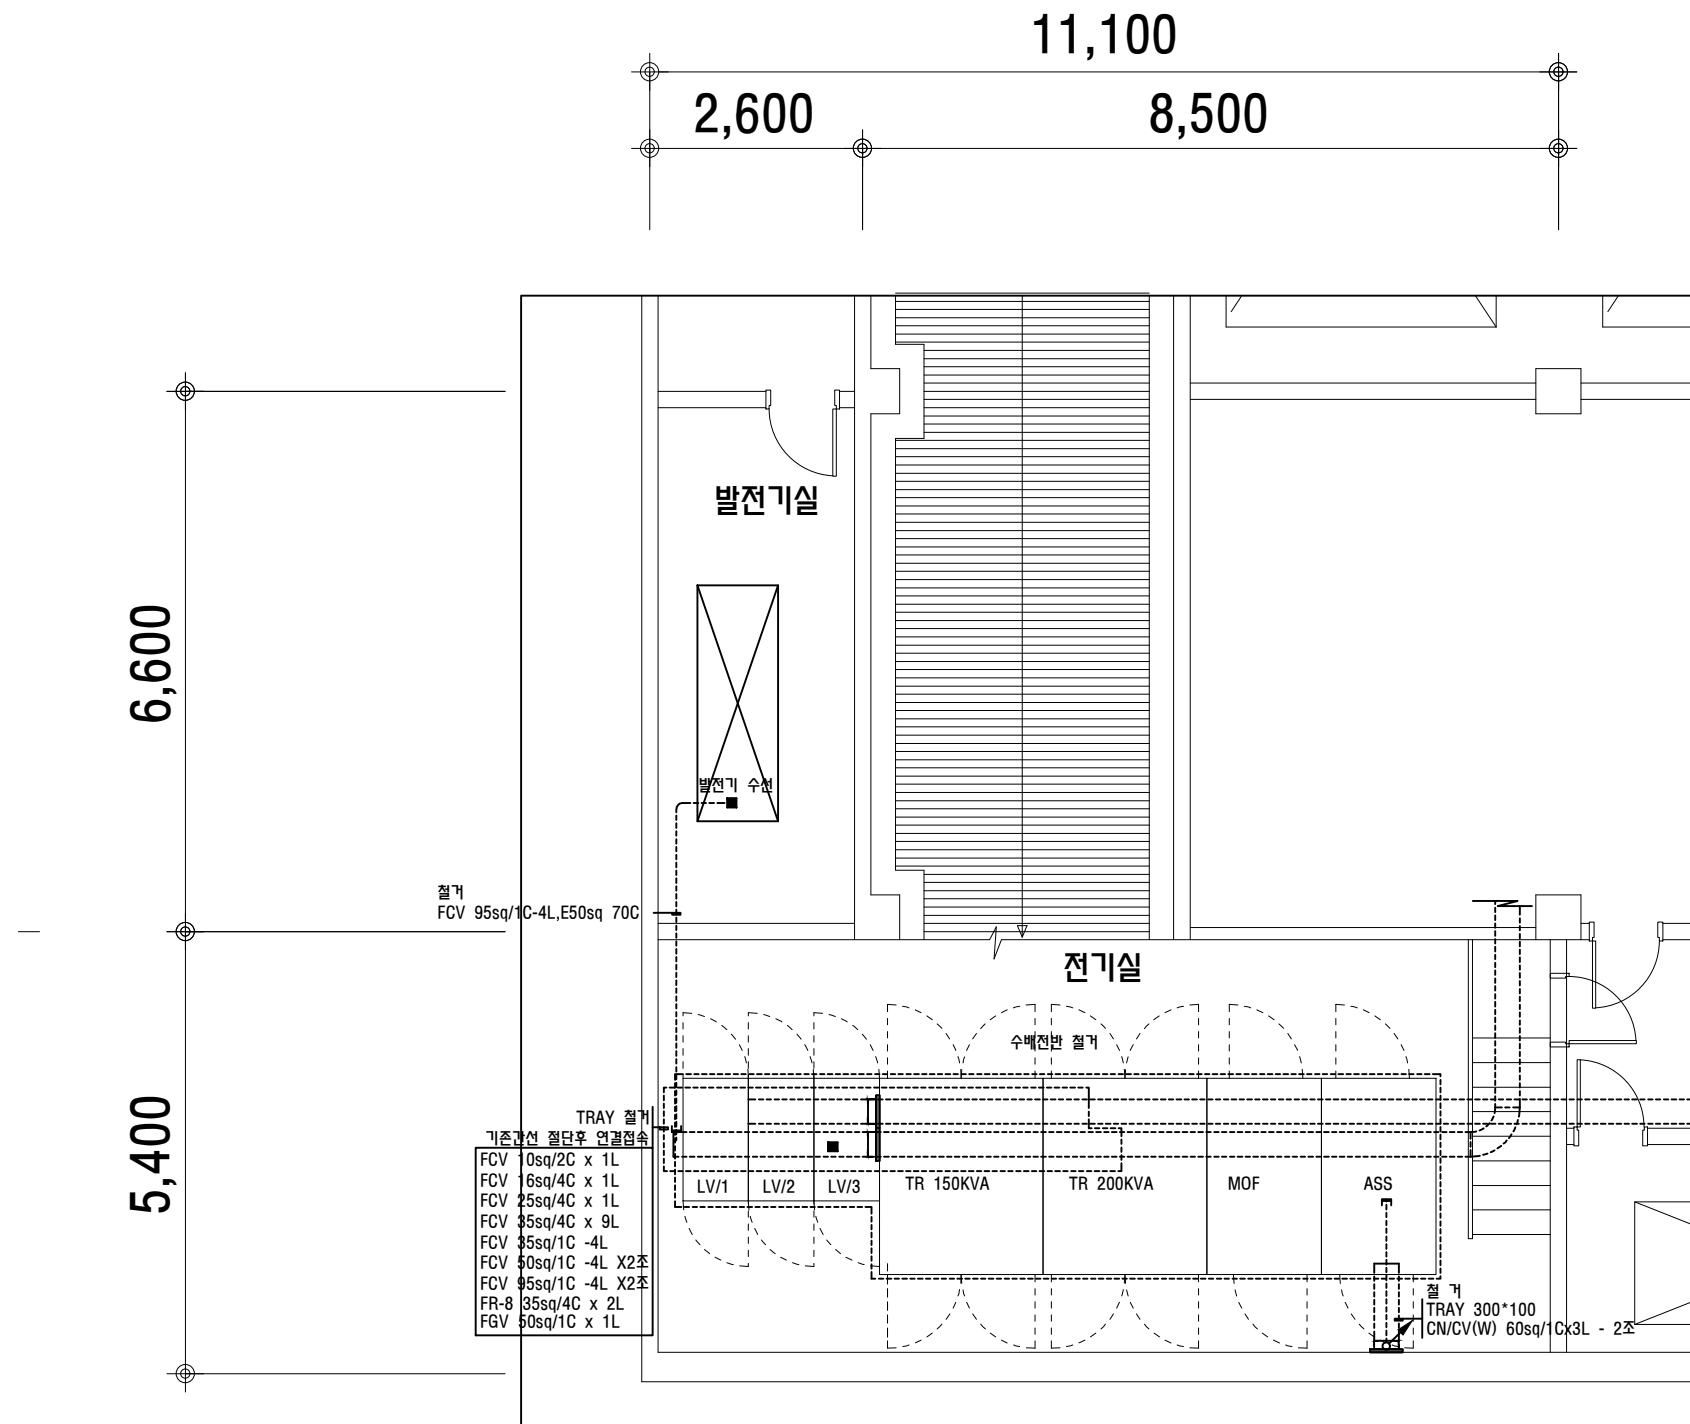



지하층 전기실 평면도
(변경전)

SCALE : A3=1/100
A1=1/50

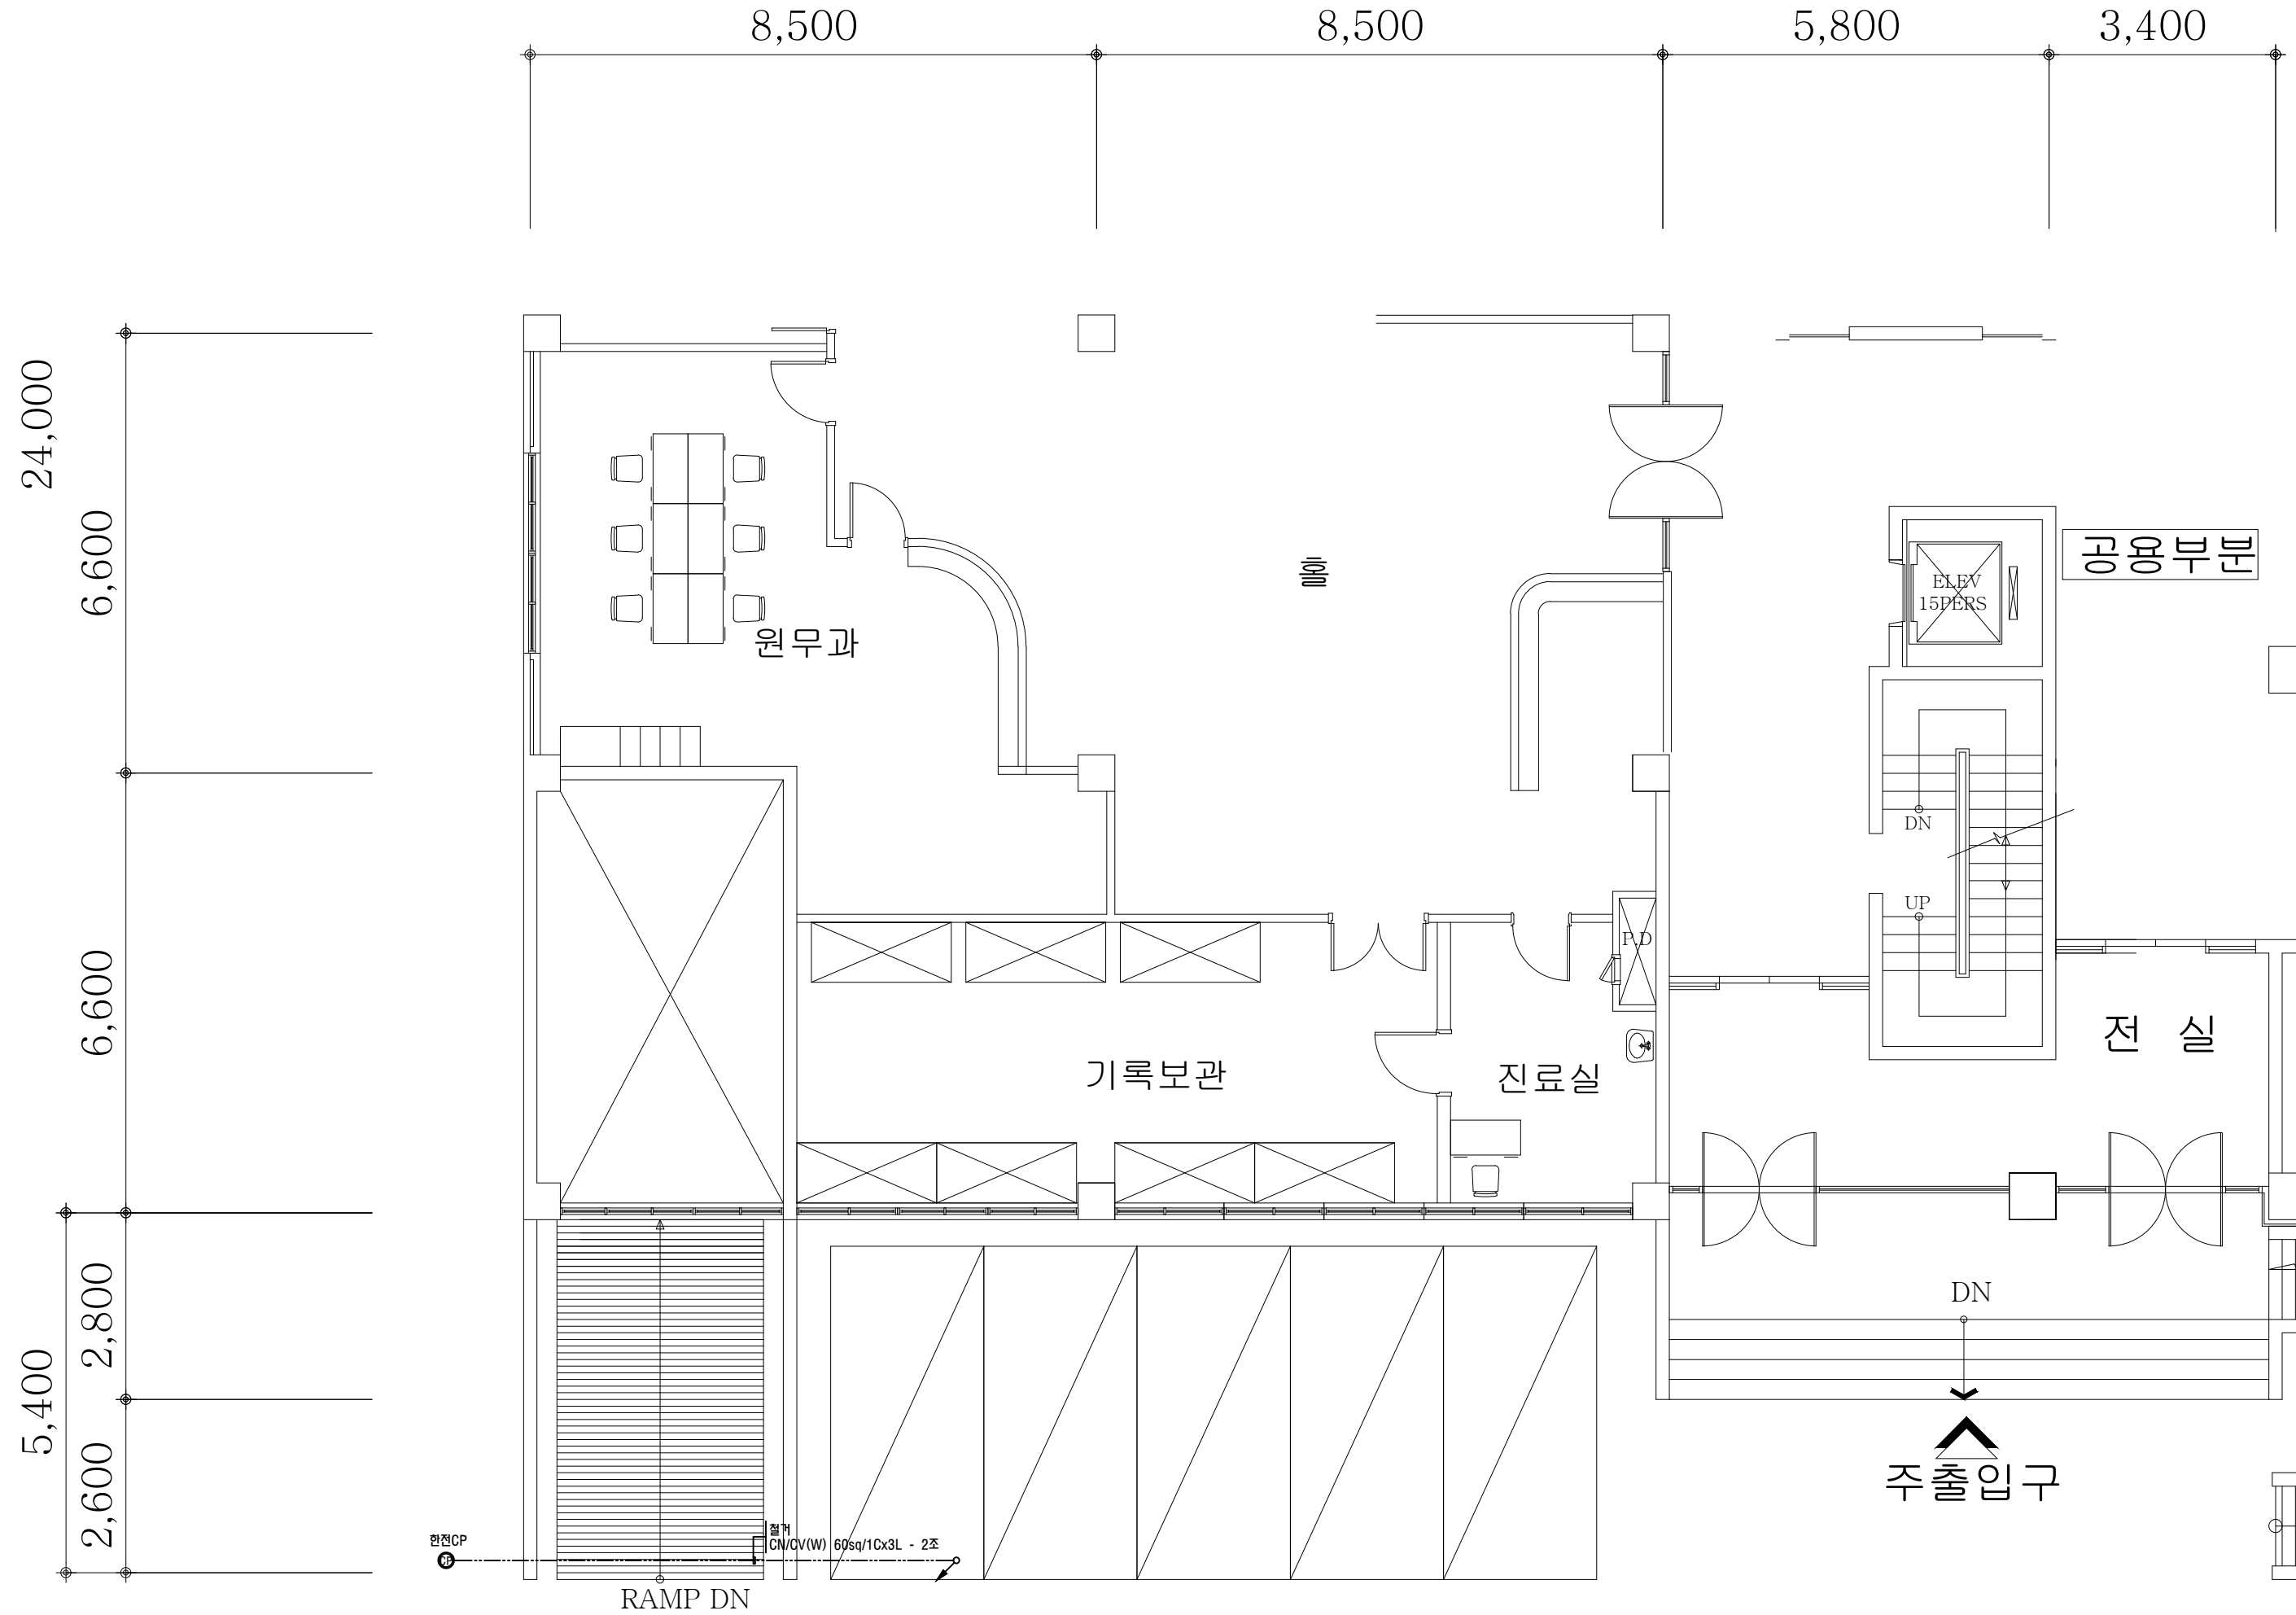


전기실 평면도
(변경전)

SCALE : A3=1/100
A1=1/50

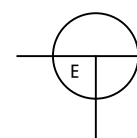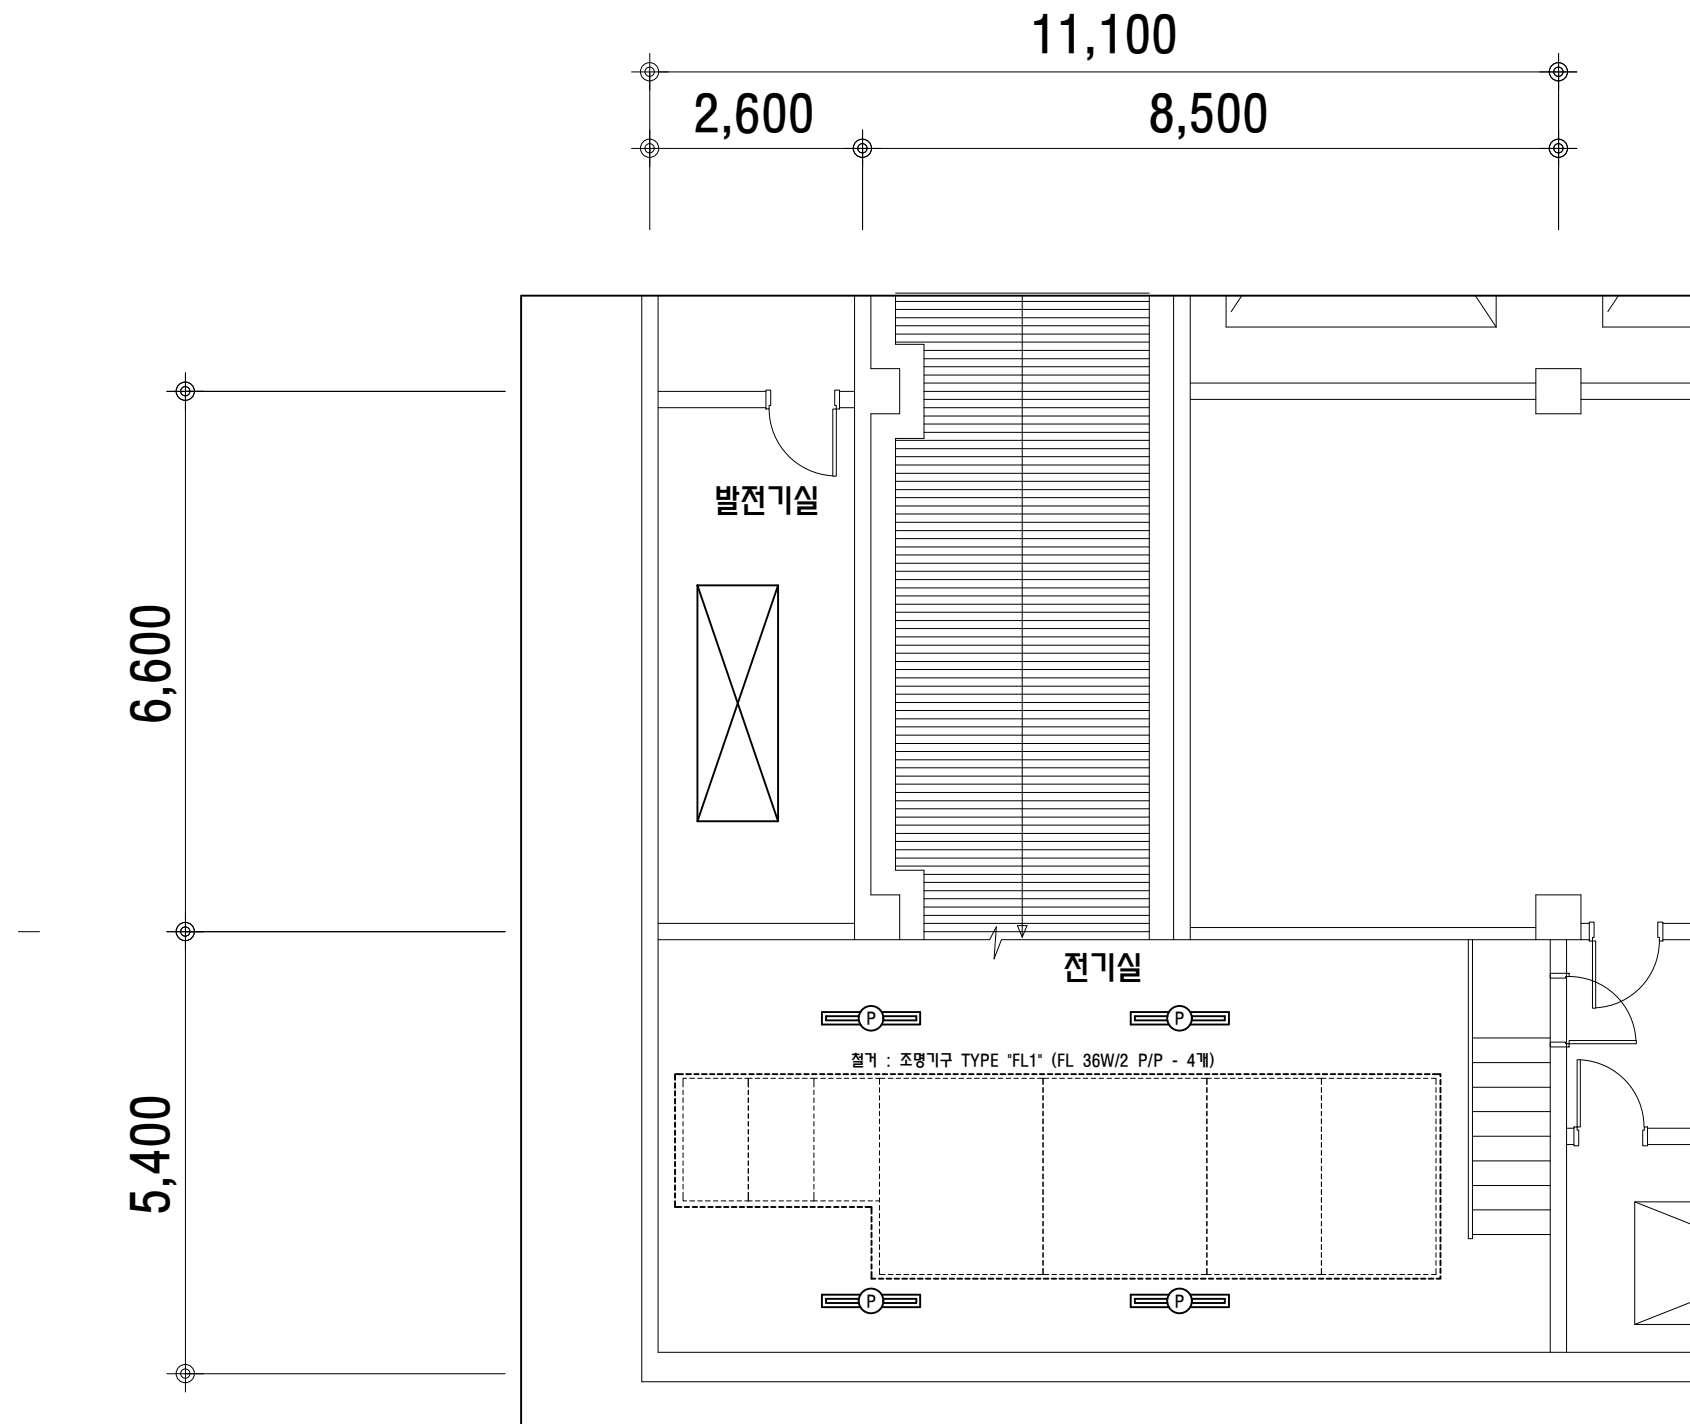


전기실 전등설비 평면도
(변경전)


SCALE : A3=1/100
A1=1/50

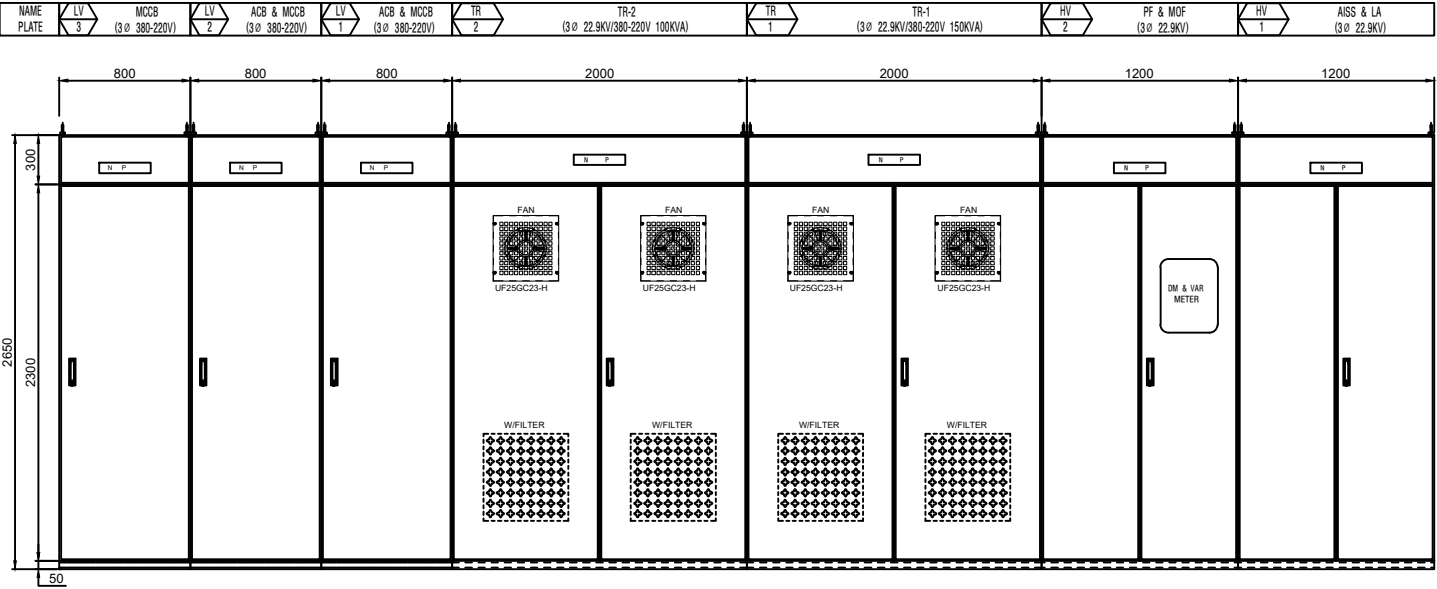


REAR VIEW

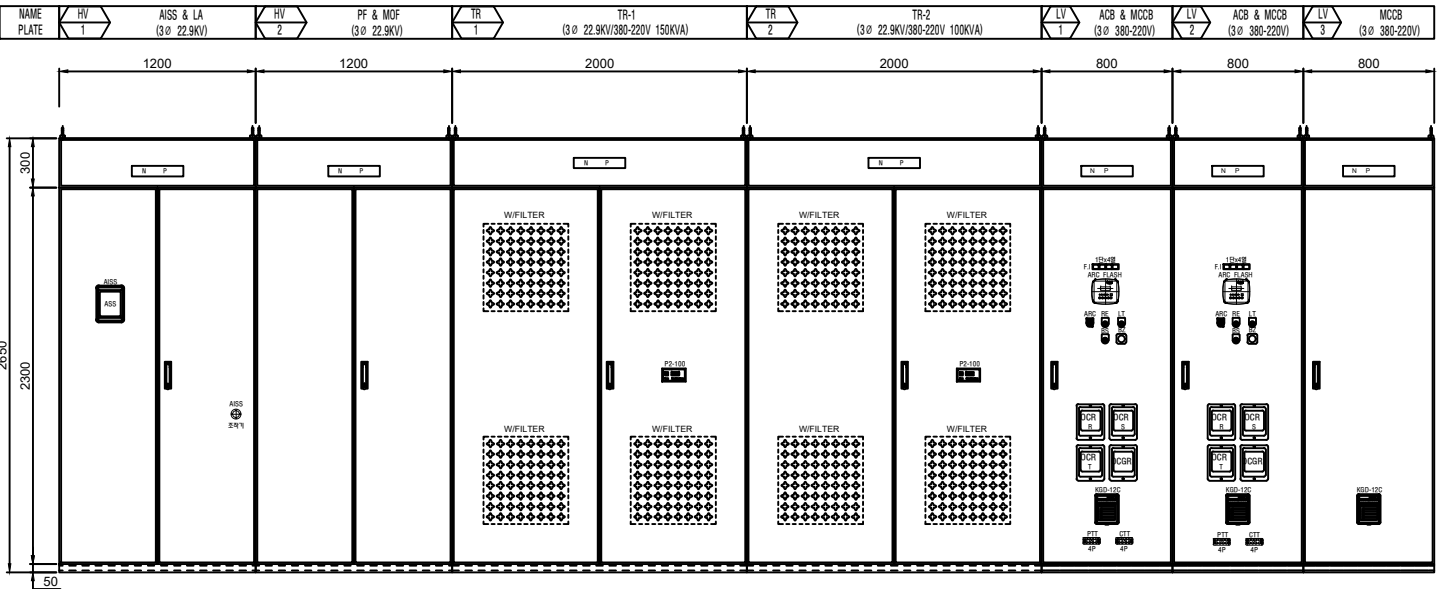

FRONT VIEW

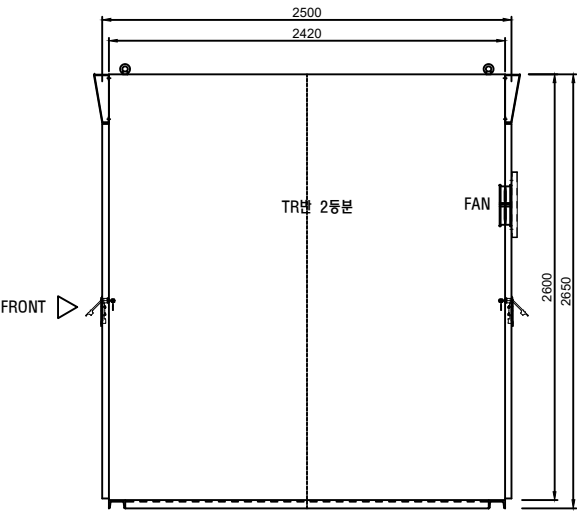


SIDE VIEW

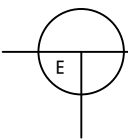

수배전반 외함상세도
(변경전)

SCALE : A3=NONE
A1=NONE


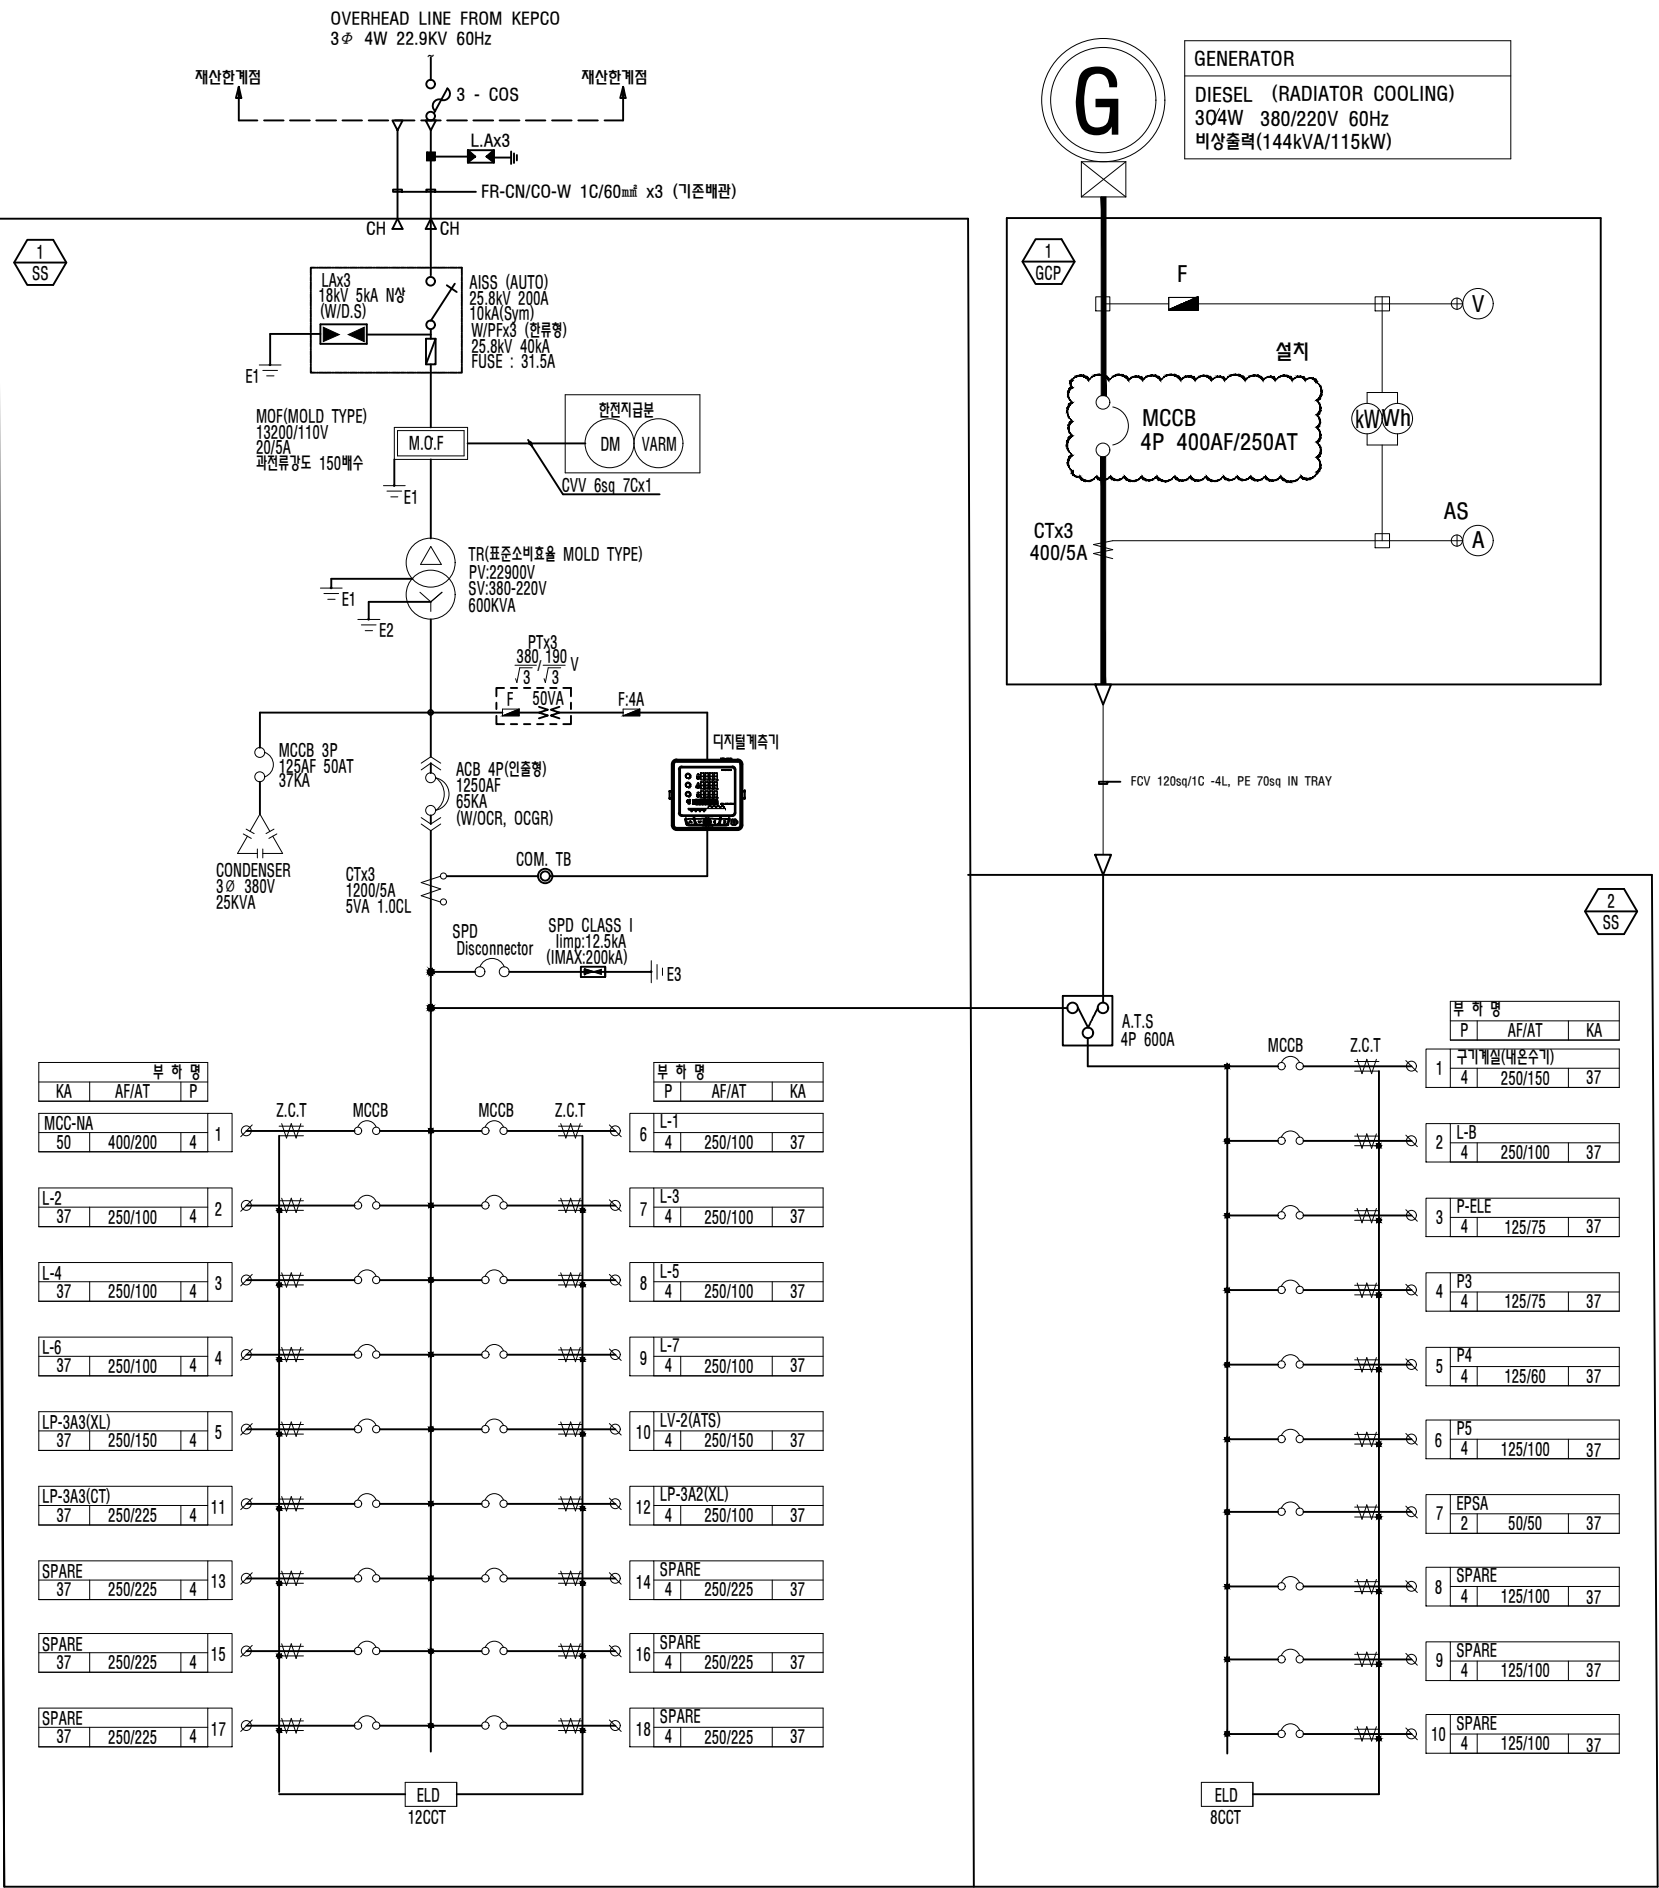


점지용 배관배선 규격

번호	적용기기	보호도제	배관규격	비고
1	파뢰기(LA)	FGV 35sq	28C(HI)	
2	특고압기기, 특고압배전반	FGV 35sq	28C(HI)	
3	변압기중성점	FGV 95sq	36C(HI)	
4	저압기기외함, 저압배전반	FGV 70sq	28C(HI)	
5	보조접지	FGV 16sq	22C(HI)	2개소

*. 점지도제는 반드시 녹색 또는 녹색교체 FGV 전선을 사용하고, 해당기기에 연결시에는 TERMINAL LUG와 볼트를 사용하여 전기적으로 완전한 접속이 되도록 하여야한다.

*. 점지극은 충분한 안전 접촉전압값이 나오도록 매설 하여야 한다.

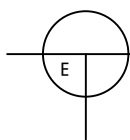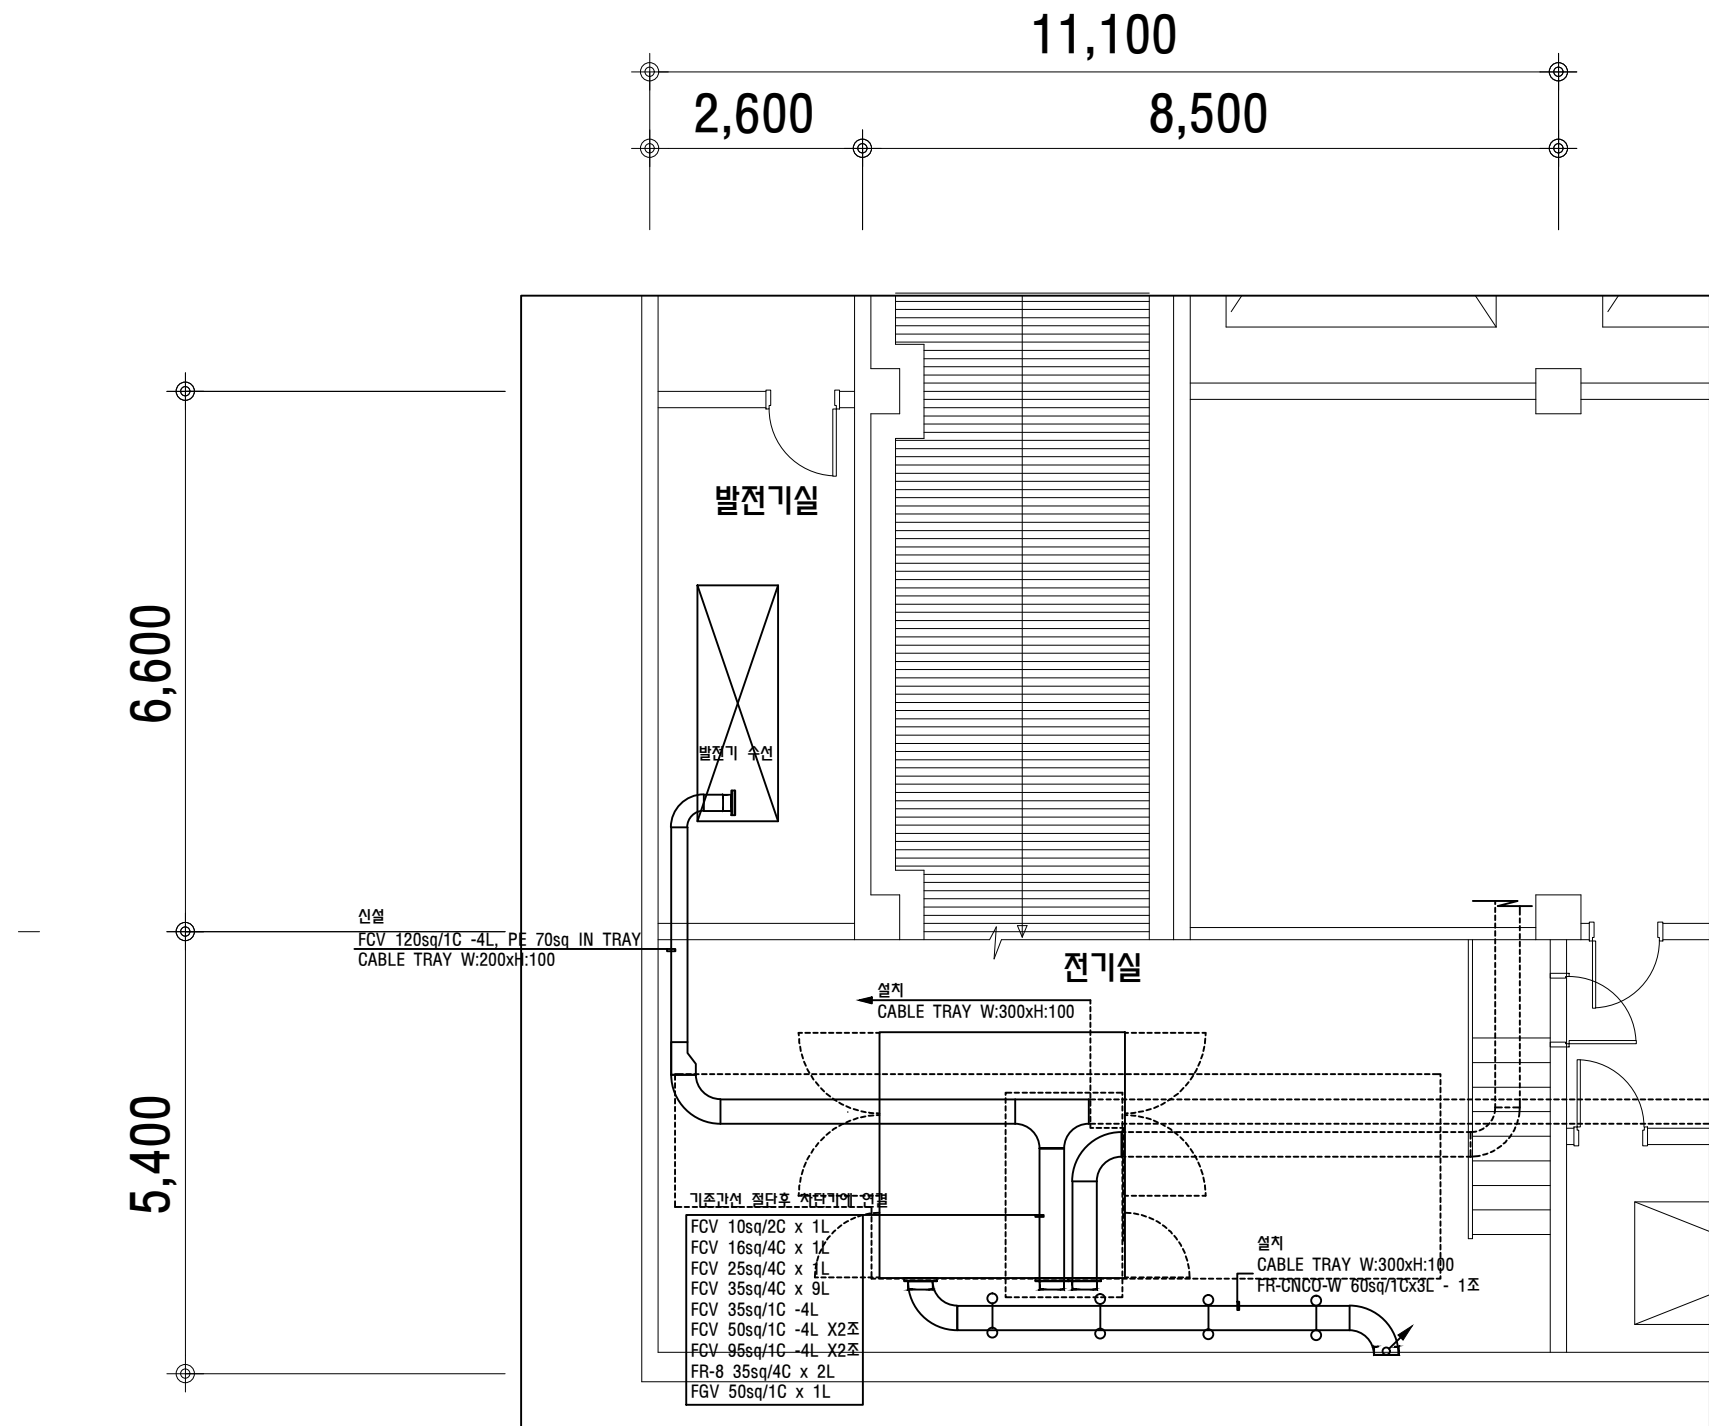

지하층 전기실 평면도
(변경후)

SCALE : A3=1/100
A1=1/50

점지용 배관배선 규격


번호	적용기기	보호도제	배관규격	비고
1	피뢰기(L.A)	FGV 35sq	28C(HI)	
2	특고압기기, 특고압배전반	FGV 35sq	28C(HI)	
3	변압기중성점	FGV 95sq	36C(HI)	
4	저압기기위함, 저압배전반	FGV 70sq	28C(HI)	
5	보조점지	FGV 16sq	22C(HI)	2개소



*. 점지도제는 반드시 녹색 또는 녹황교제 FGV 전선을 사용하고,

해당기기에 연결시에는 TERMINAL LUG와 볼트를 사용하여

전기적으로 완전한 접속이 되도록 하여야한다.



*. 기존 전기도제에 보강공사

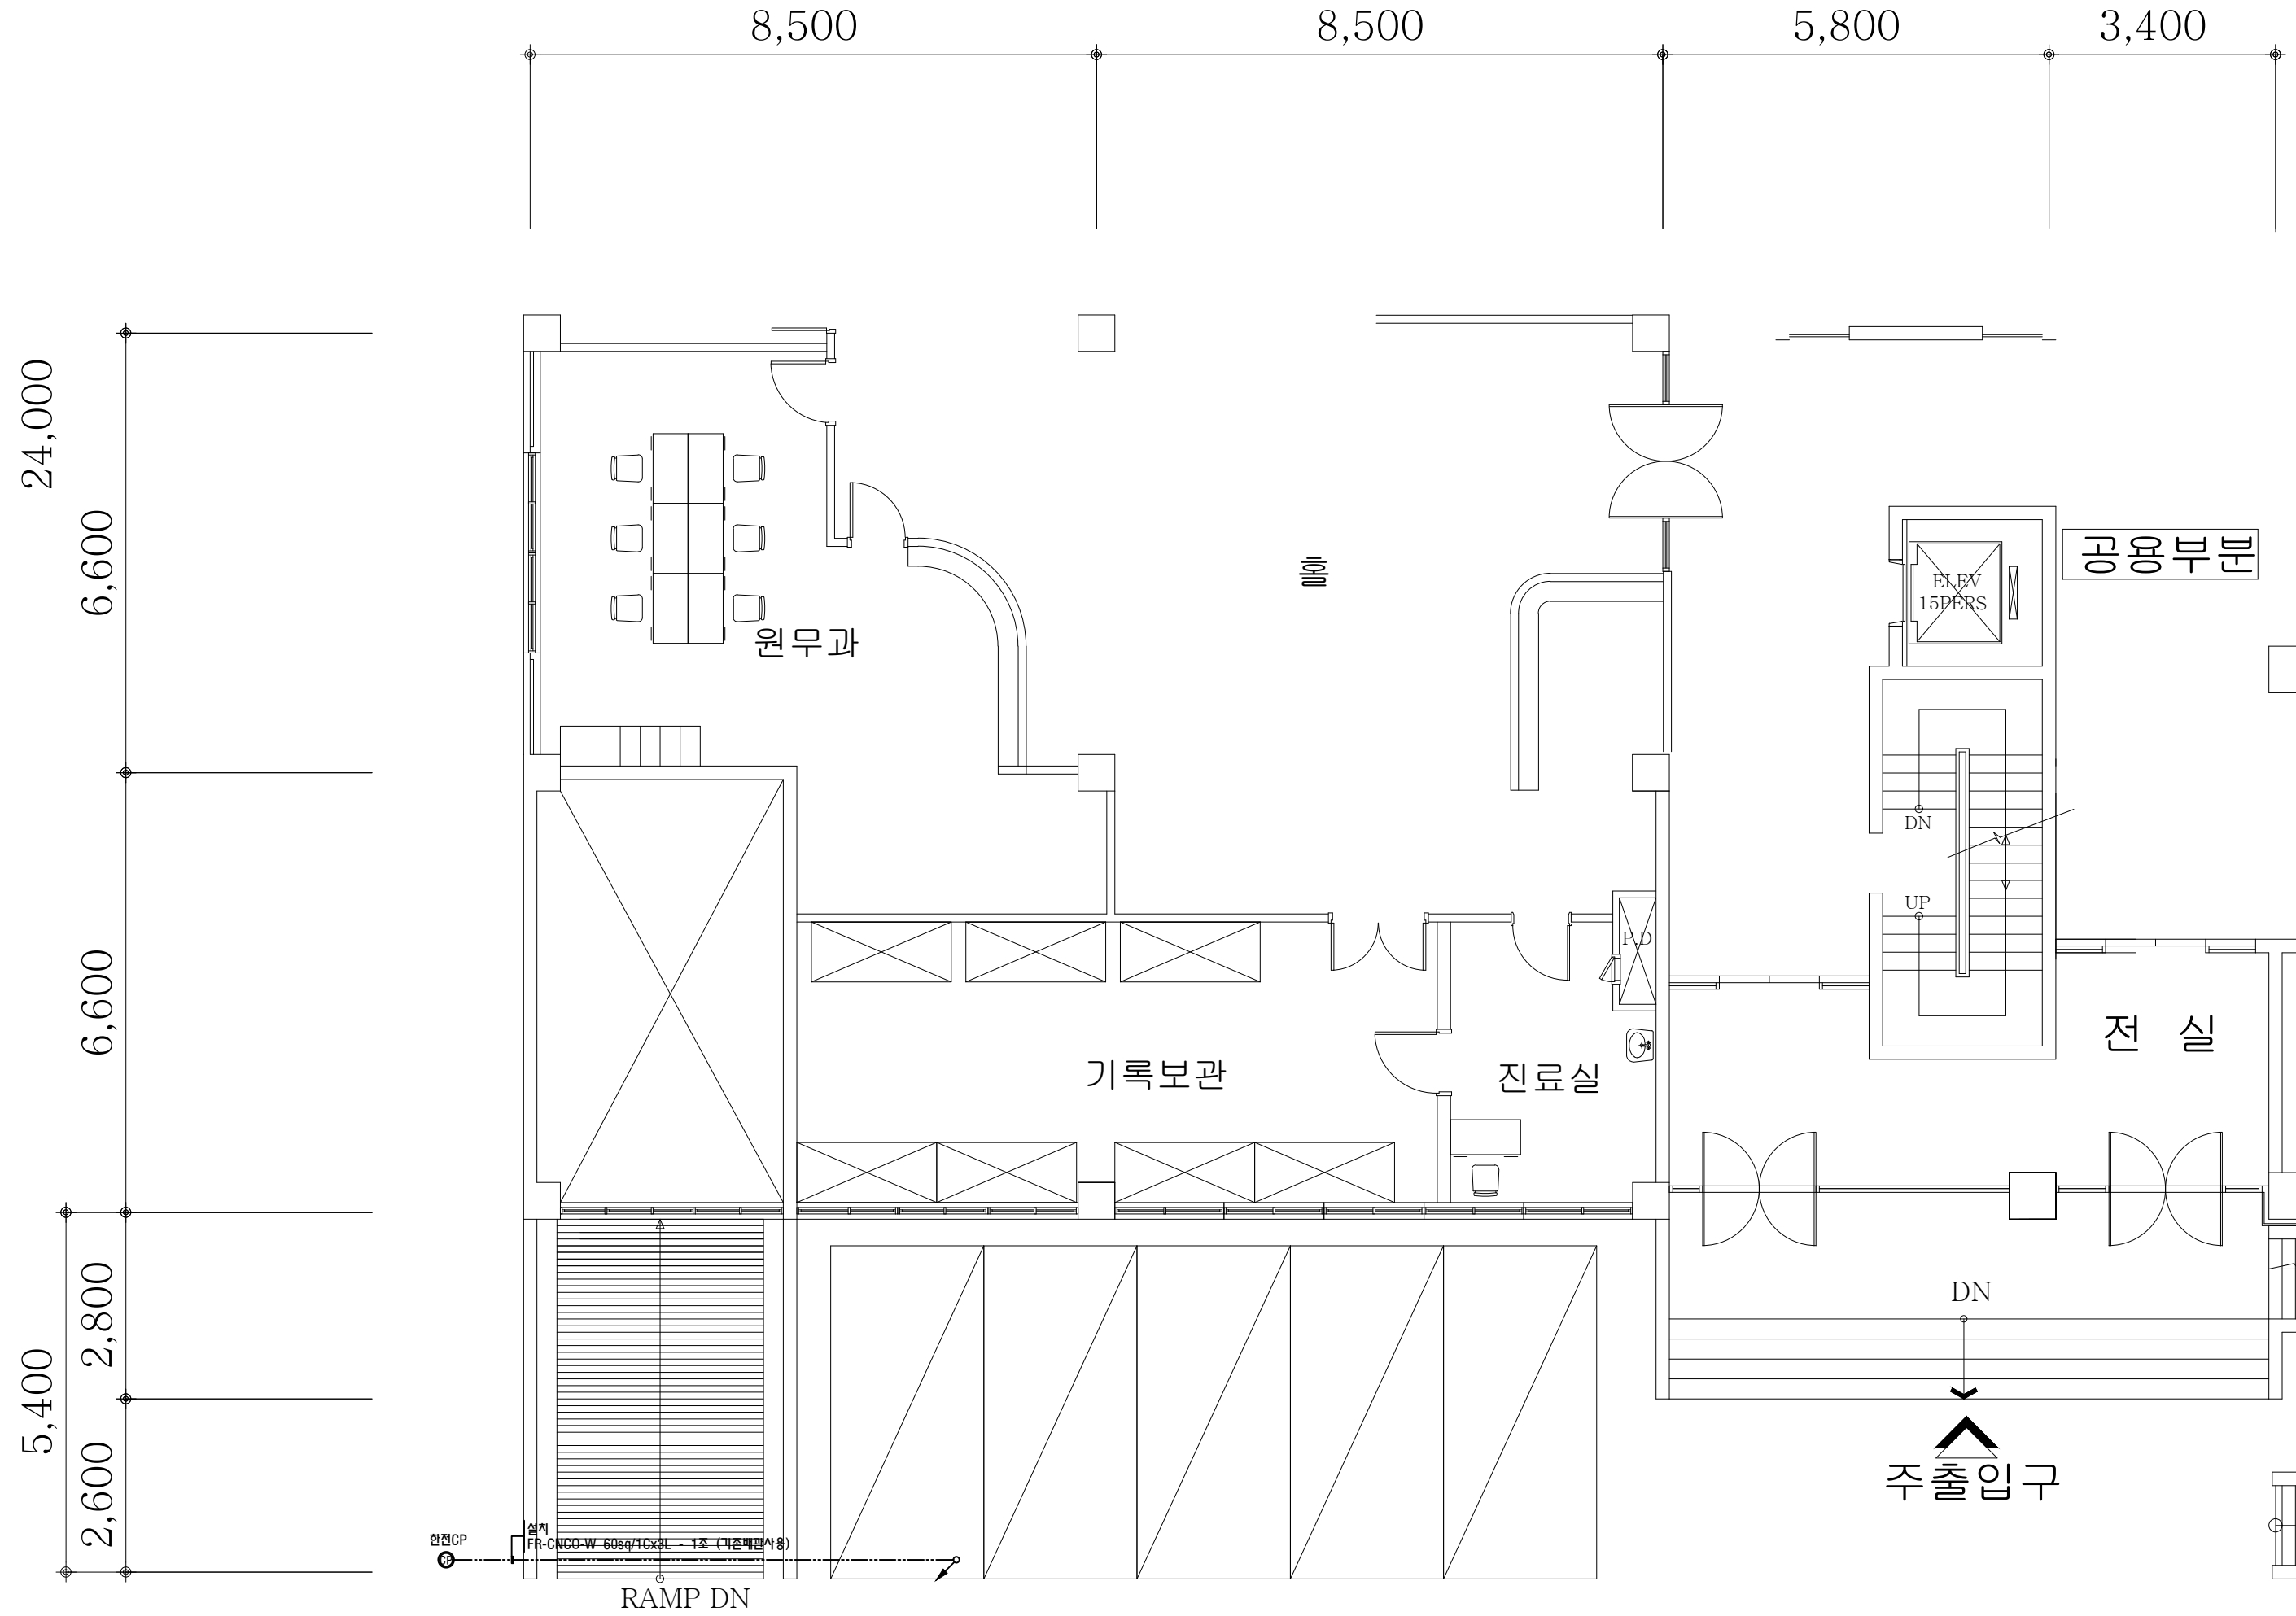

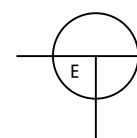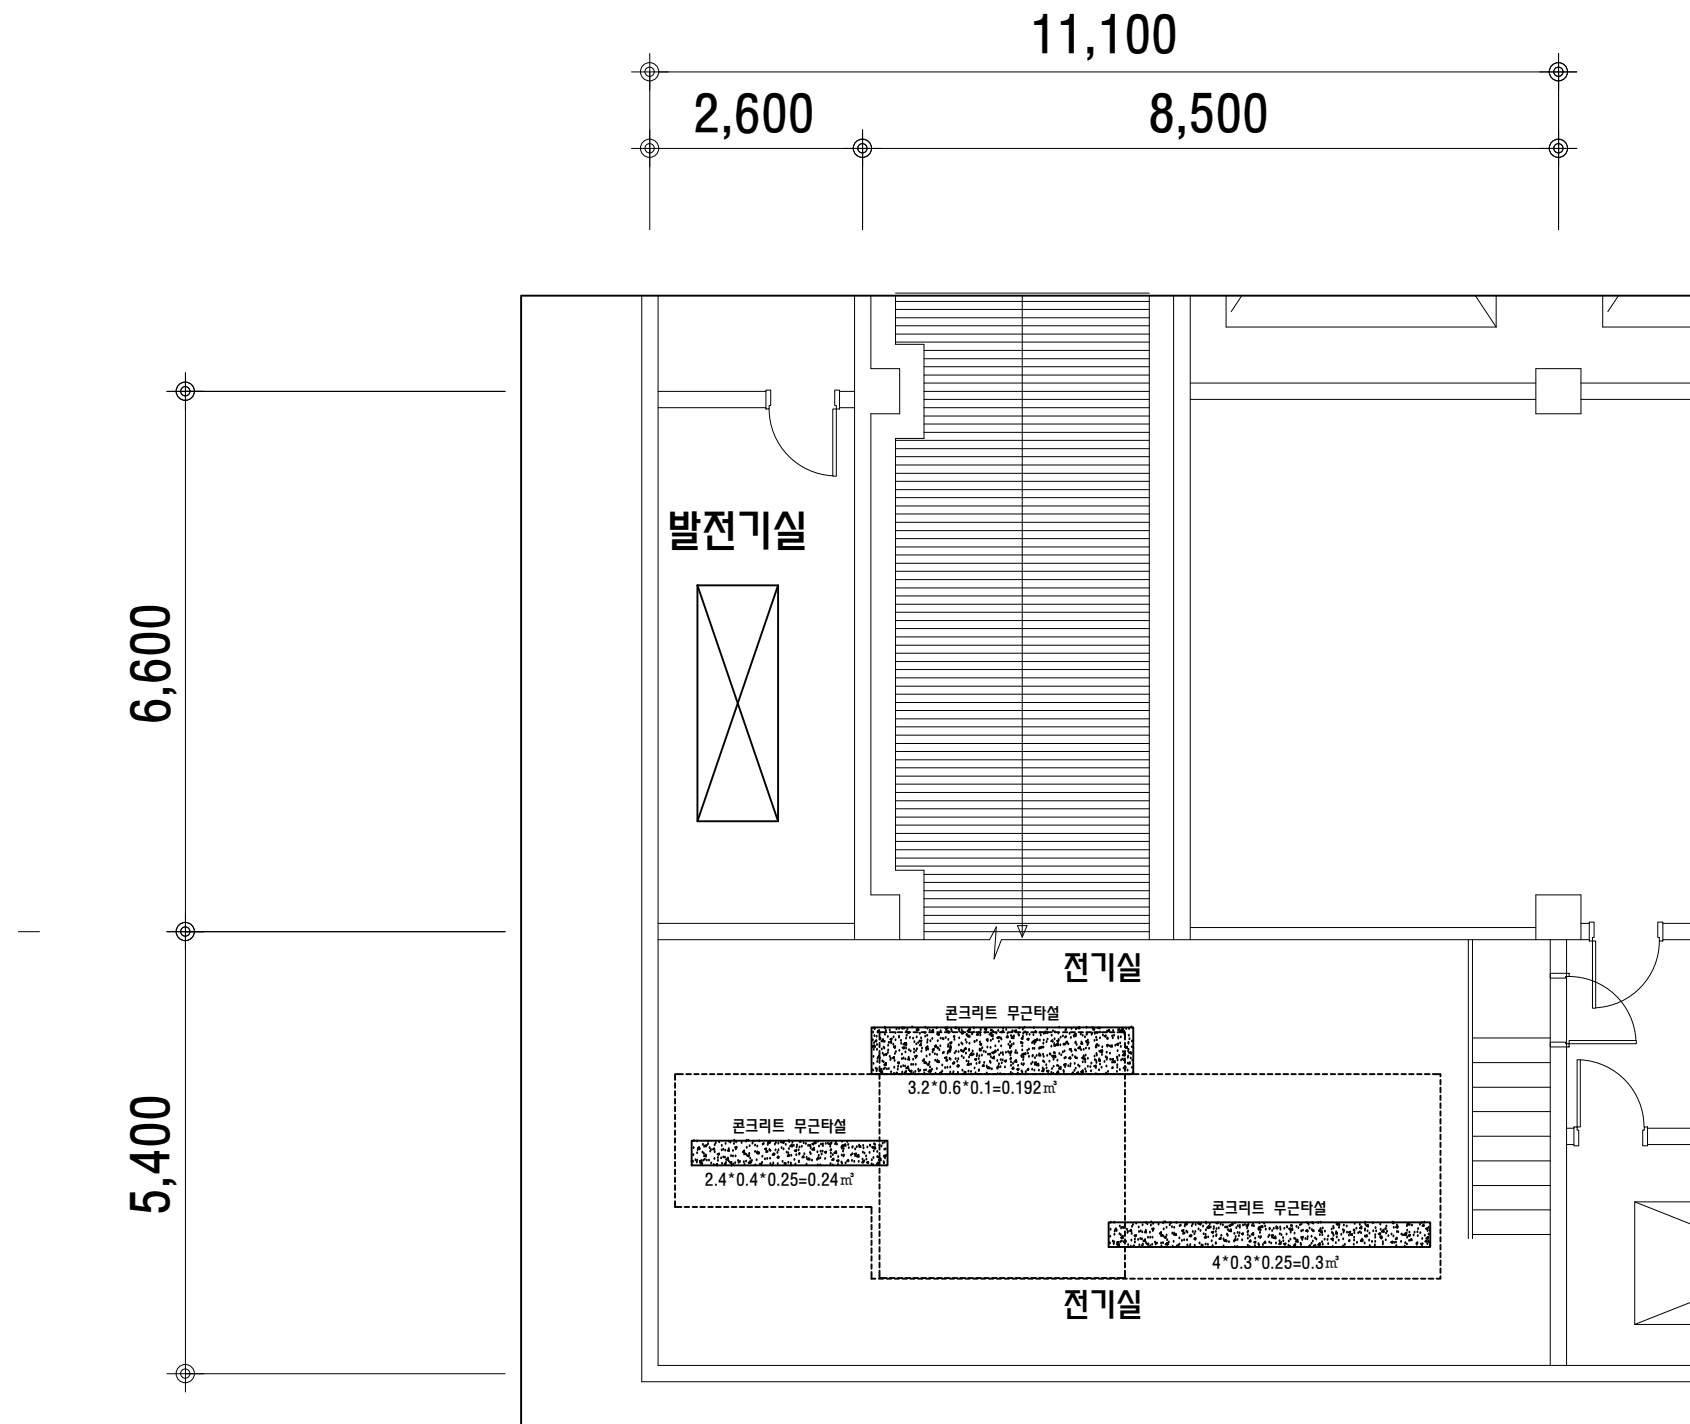


전기실 기초 평면도
(변경후)

SCALE : A3=1/100
A1=1/50

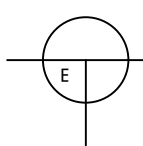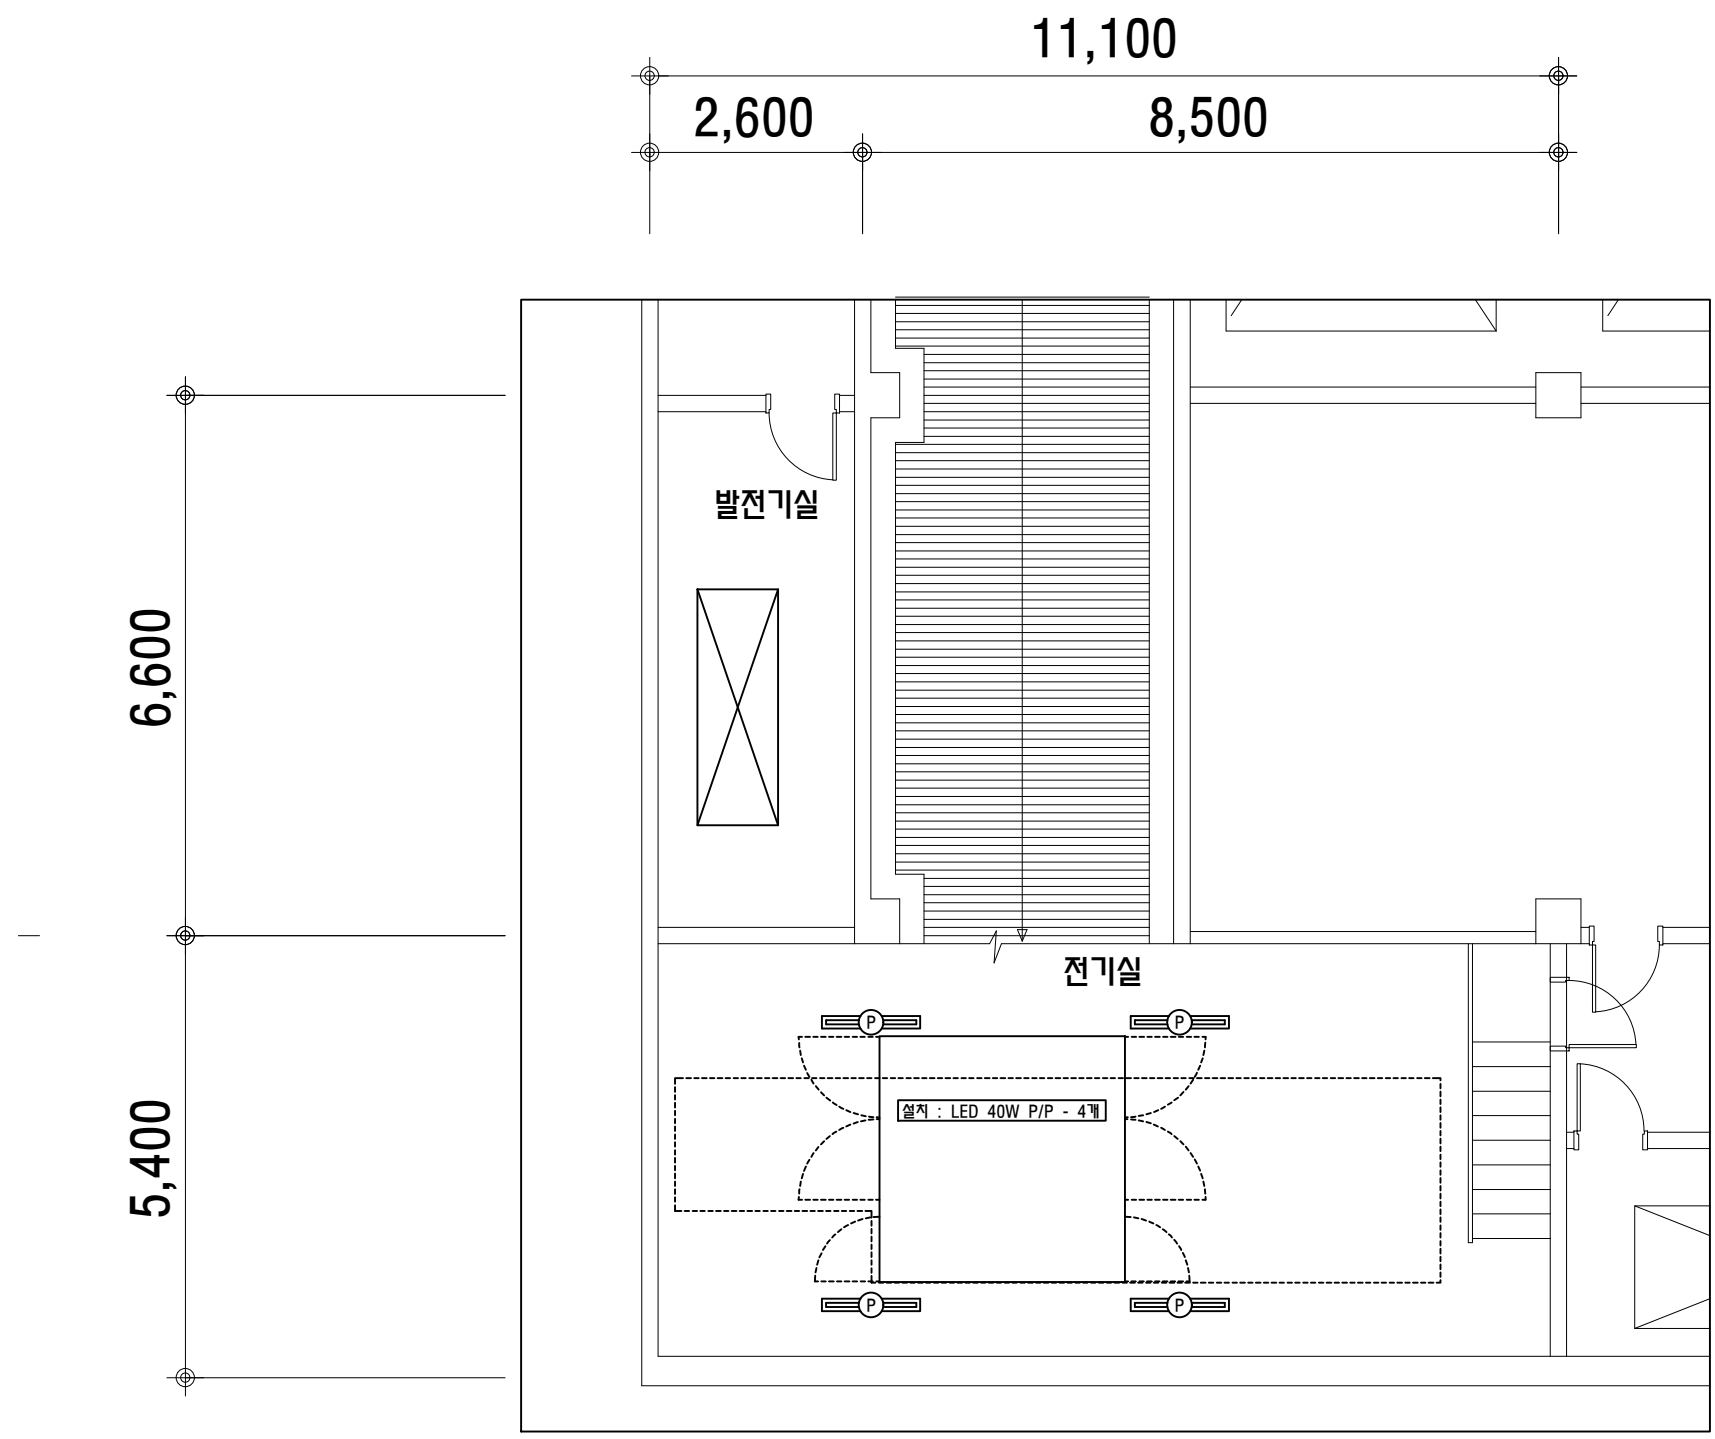

전기실 전등설비 평면도
(변경후)






SCALE : A3=1/100
A1=1/50

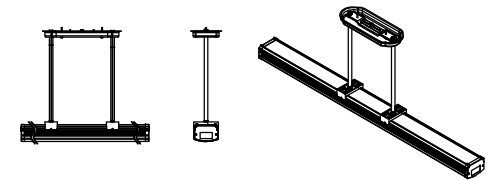


명칭	재질 및 색상/마감	수량
몸체	알루미늄 SHEET	1
램프	LED 40W	1
색온도	6000K(CW), 3200K (WW), 70Ra	1
카바	광확산 P.C 1.5mm	1

1200*100

TYPE- L1 (LED 40W, 파이프펜던트형)

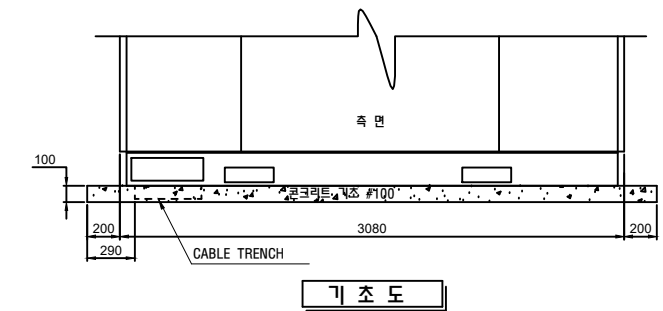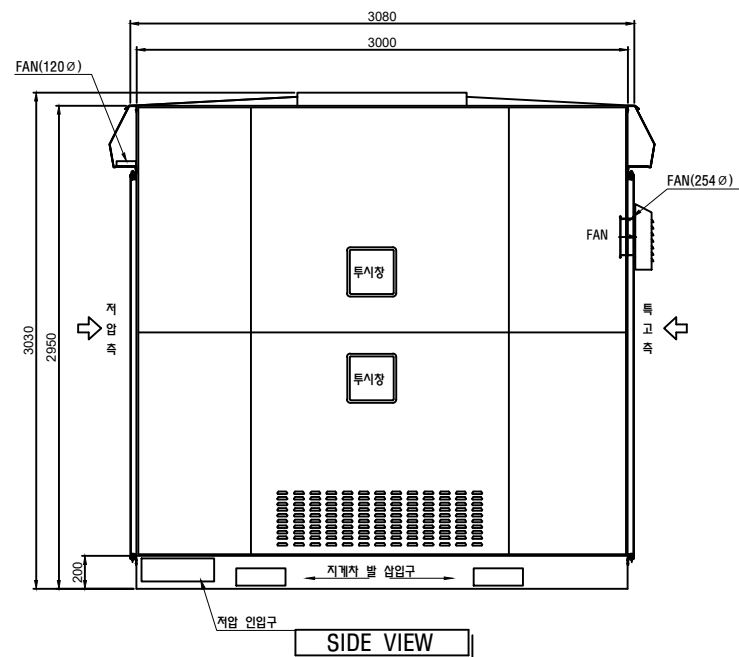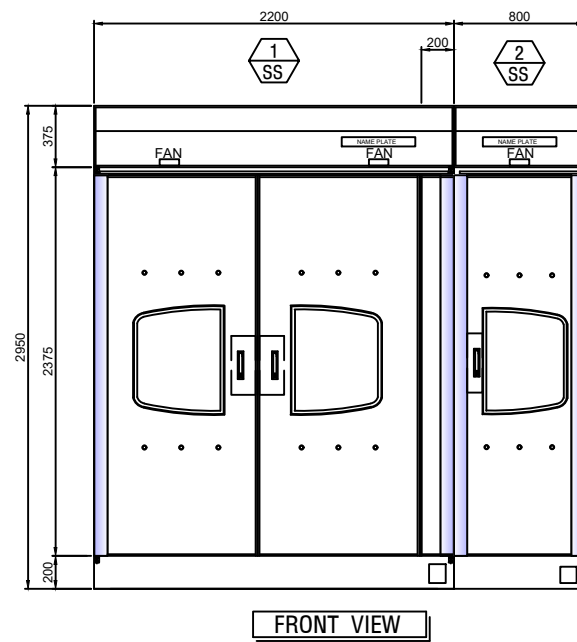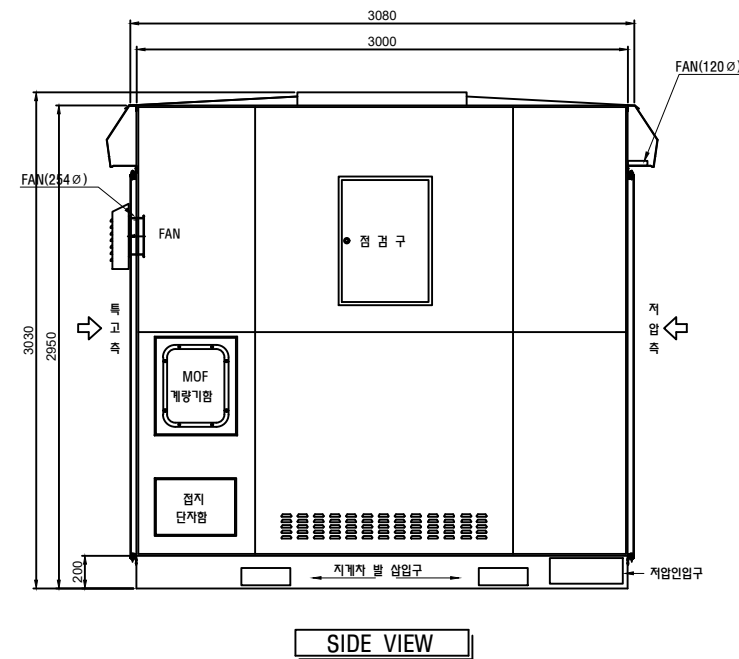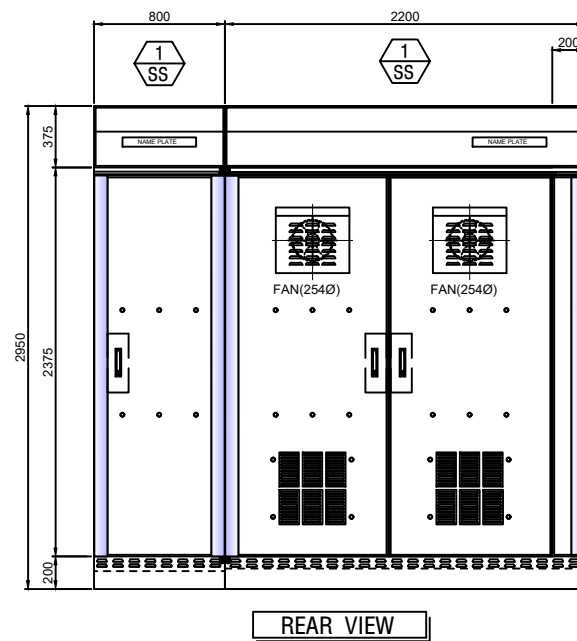

- * NOTE *
1. 도장 색상
 - 1) 외 부 : 아이보리 (MUNSELL NO. 5Y 7/1)
 - 2) BASE : 아이보리 (MUNSELL NO. 5Y 7/1)
 - 3) 내부DOOR : 아이보리 (MUNSELL NO. 5Y 7/1)
 - 4) 상부(이마) : 아이보리 (MUNSELL NO. 5Y 7/1)
 - 5) 외부 DOOR : STEEL
 - 6) 후면 P-COVER : STEEL

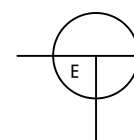

수배전반 외함상세도
(변경후)

SCALE : A3=NONE
A1=NONE