



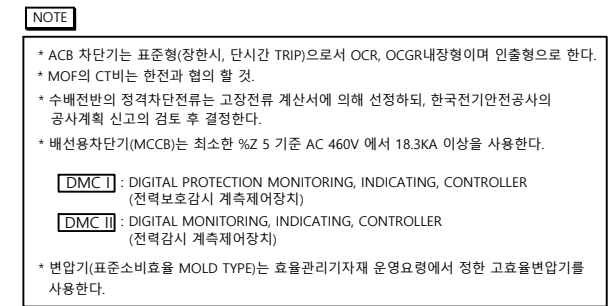

1 수변전설비 단선 결선도

(주) 신화엔지니어링 종합건축사사무소
전 문 설 계 업 1 종 제 1-2-12 호
발송배전기술사 오 정 근 (인)
대전광역시 동구 유전동 143-21번지 TEL:(042) 670-3191~4

<b style="font-size: 1.2em;">DCCO <b style="font-size: 1.2em;">대전도시공사			
PROJECT TITLE			
대동지식산업센터 전기공사			
DESIGN FIRM			
(주) 디엔비건축사사무소 TEL: 042) 823-3724 FAX: 042) 823-9820 Http://WWW.dnbarch.co.kr			
<b style="font-size: 2em;">SHINHWA ENGINEERING ARCHITECTURE TEL: 042) 670-3175 FAX: 042) 670-3149 Http://WWW.sh-eng.com			
NOTE			
△			
△			
△			
NO.	DATE	REV.DES/DESCRIPTION	APPR.
DRAWING TITLE			
수변전설비 단선 결선도			
APPROVED			
CHECKED 2			
CHECKED 1			
DRAWN BY			
SCALE		APPROVAL DATE	
A1	A3	2017. 08.	
1 / NONE 1 / NONE			
DRAWING NO.			REV.
E - 관급 002			

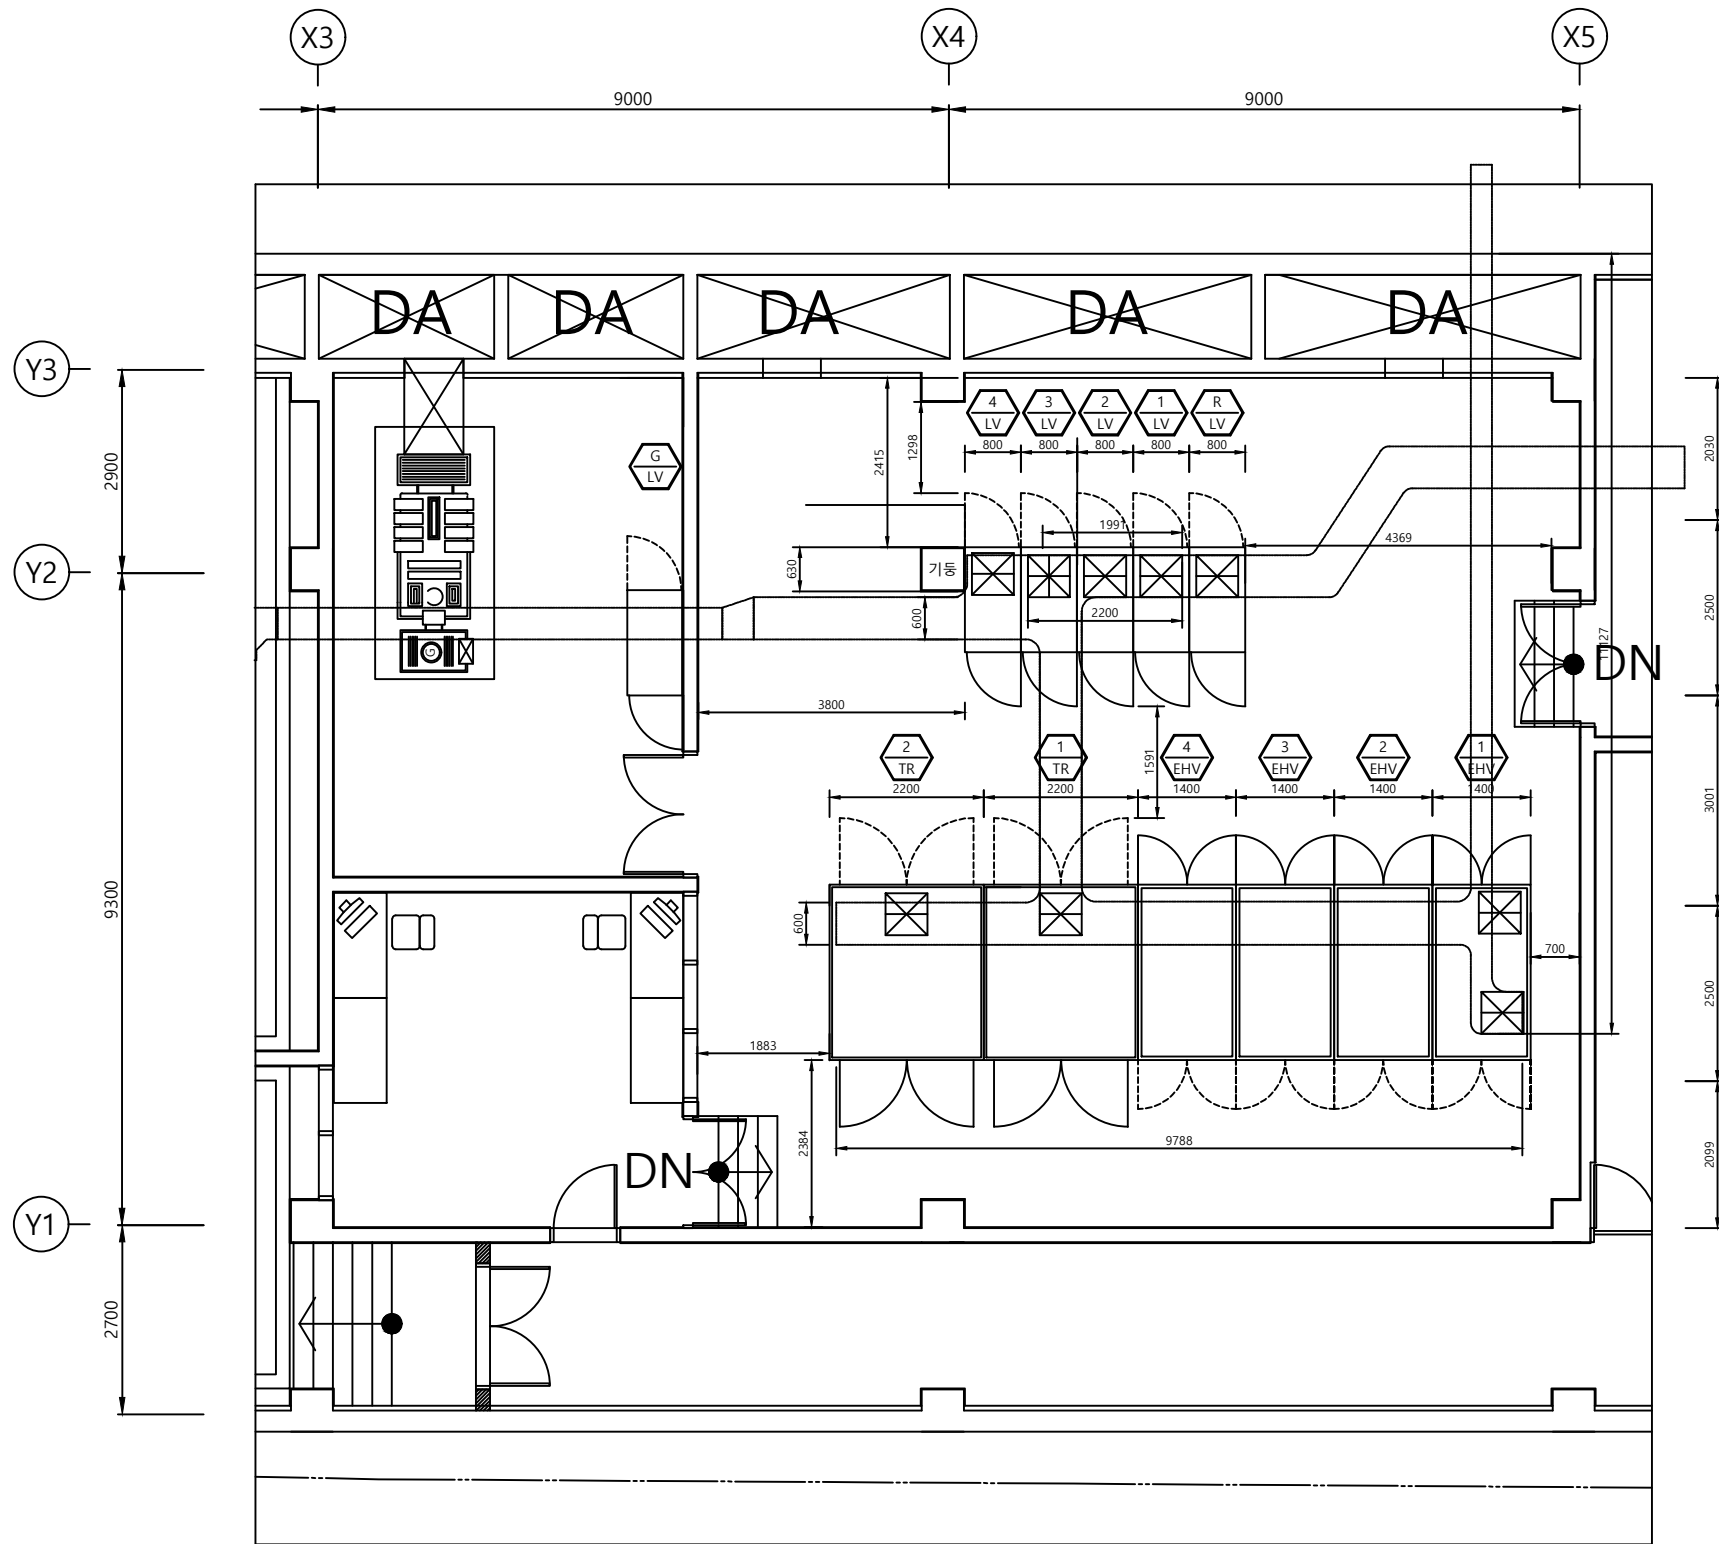

1 전기실 기기배치 확대 평면도
S=A1:1/50, A3:1/100

(주) 신화엔지니어링 종합건축사사무소
전 문 설 계 업 1 종 제 1-2-12 호
발송배전기술사 오 정 근 (인)
대전광역시 동구 용전동 143-21번지 TEL:(042) 670-3191~4



PROJECT TITLE
대동지식산업센터
전기공사

DESIGN FIRM
 (주) 디엔비건축사사무소
 TEL: 042) 823-3724 FAX: 042) 823-9820
 Http://WWW.dnbarch.co.kr

SHINHWA
ENGINEERING | ARCHITECTURE
 TEL: 042) 670-3175 FAX: 042) 670-3149
 Http://WWW.sh-eng.com





NOTE

△					
△					
△					
NO.	DATE	REV.	DESCRIPTION	APPR.	




DRAWING TITLE
전기실 기기배치 확대 평면도

APPROVED
 CHECKED 2
 CHECKED 1
 DRAWN BY

SCALE		APPROVAL DATE	
A1	A3	2017. 08.	
1 / 50	1 / 100		
DRAWING NO.		REV.	
E - 관급 003			

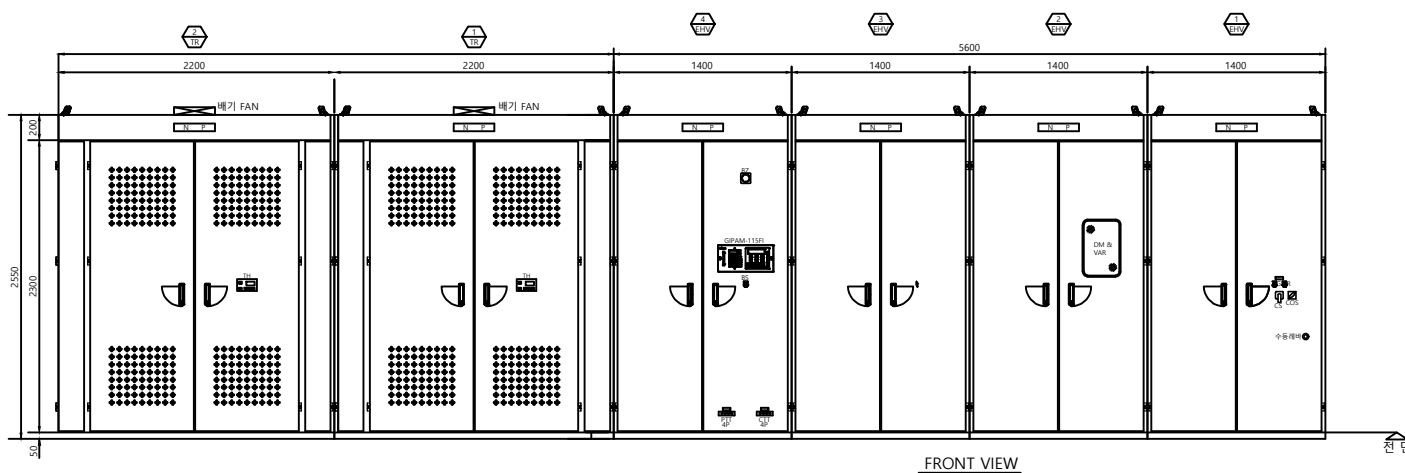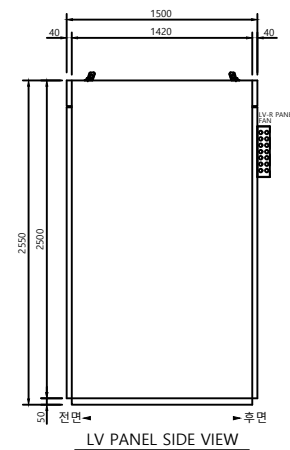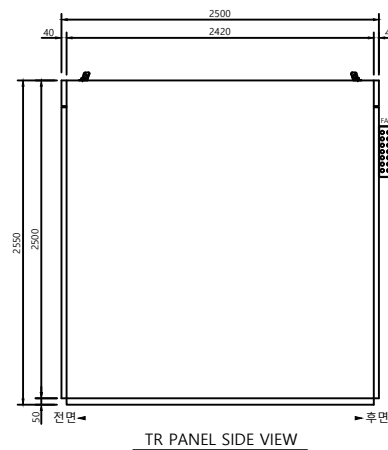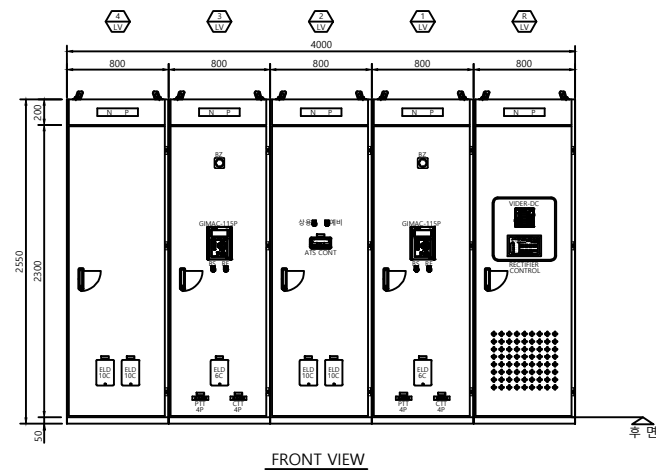

NOTE		
1	구 조	육내 노출자립형
2	FRAME	BOLT 조립식 ANGLESS TYPE 3.2t
3	DOOR	전후면 STEEL 3.2t
4	SIDE	STEEL 2.0t
5	TOP	STEEL 2.0t
6	BASE	5x100x50mm (ㄷ형강)
7	COLOR	MUNSELL NO. 5Y 7/1
8	PL,PB	30mm

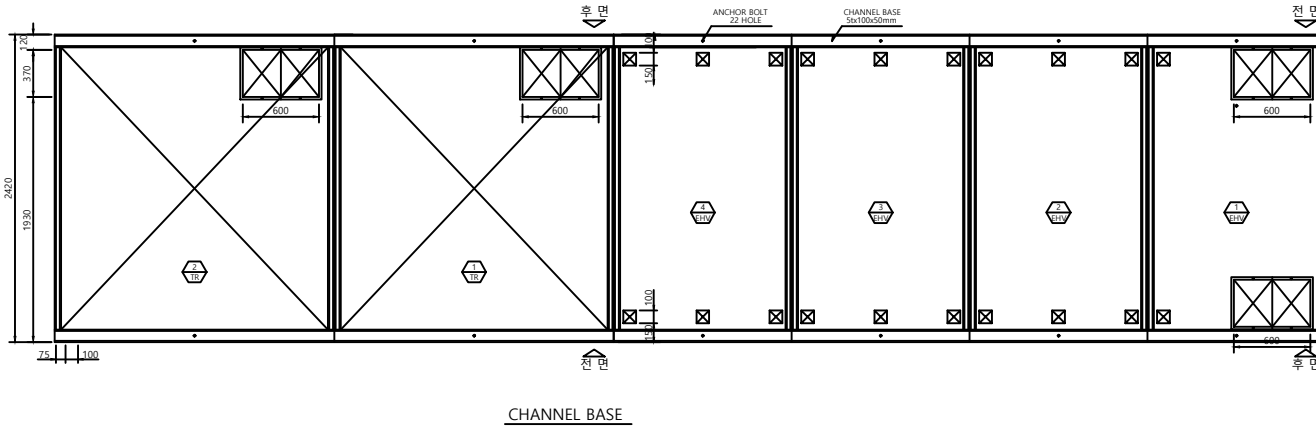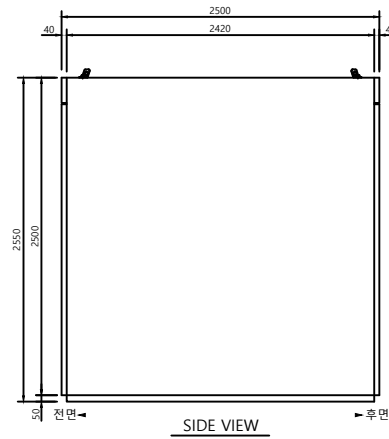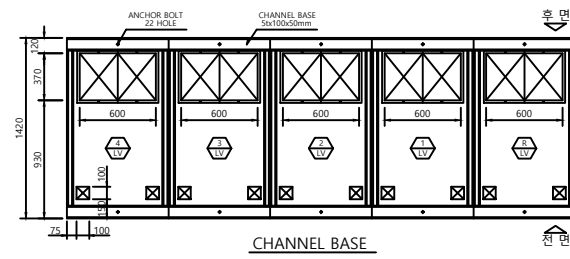

NOTE		
1	구 조	육내 노출자립형
2	FRAME	BOLT 조립식 ANGLESS TYPE 3.2t
3	DOOR	전후면 STEEL 3.2t
4	SIDE	STEEL 2.0t
5	TOP	STEEL 2.0t
6	BASE	5x100x50mm (ㄷ형강)
7	COLOR	MUNSELL NO. 5Y 7/1
8	PL,PB	30mm

1 수변전설비 외함상세도
S=A1:1/NONE, A3:1/NONE

(주) 신화엔지니어링 종합건축사사무소
전문설계업 1종 제 1-2-12 호
발송배전기술사 오 정 근 (인)
대전광역시 동구 용전동 143-21번지 TEL:(042) 670-3191~4



PROJECT TITLE
대동지식산업센터
전기공사

DESIGN FIRM
(주) 디엔비건축사사무소
TEL: 042) 823-3724 FAX: 042) 823-9820
Http://WWW.dnbarch.co.kr

SHINHWA
ENGINEERING | ARCHITECTURE
TEL: 042) 670-3175 FAX: 042) 670-3149
Http://WWW.sh-eng.com

NOTE

△			
△			
△			
NO.	DATE	REV. DESCRIPTION	APPR.



DRAWING TITLE
수변전설비 외함상세도

APPROVED
CHECKED 2
CHECKED 1
DRAWN BY

SCALE		APPROVAL DATE	
A1	A3	2017. 08.	
1 / NONE	1 / NONE		
DRAWING NO.		REV.	
		E - 관급 004	

△			
△			
△			
NO.	DATE	REV.DESCRPTION	APPR.

DRAWING TITLE MCC 결선도			
APPROVED			
CHECKED 2			
CHECKED 1			
DRAWN BY			
SCALE A1		APPROVAL DATE 2017. 08.	
1 / NONE		1 / NONE	
DRAWING NO.			REV.
E - 관급 007			

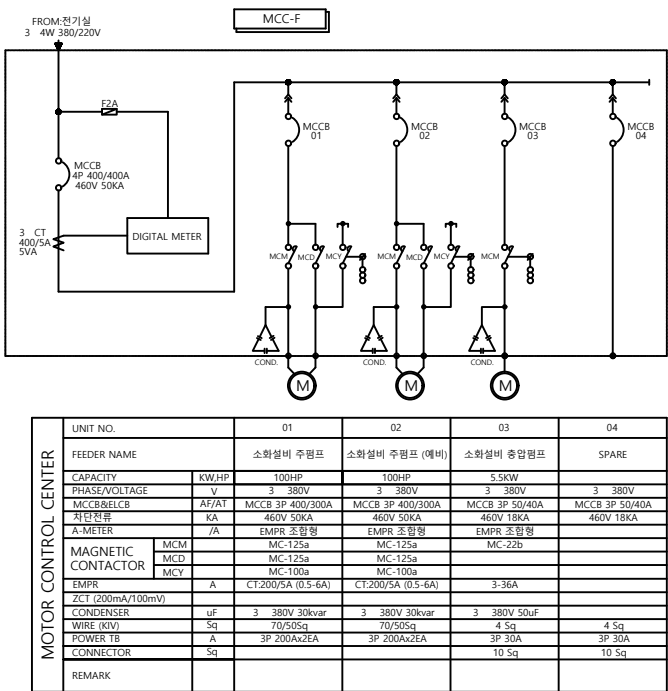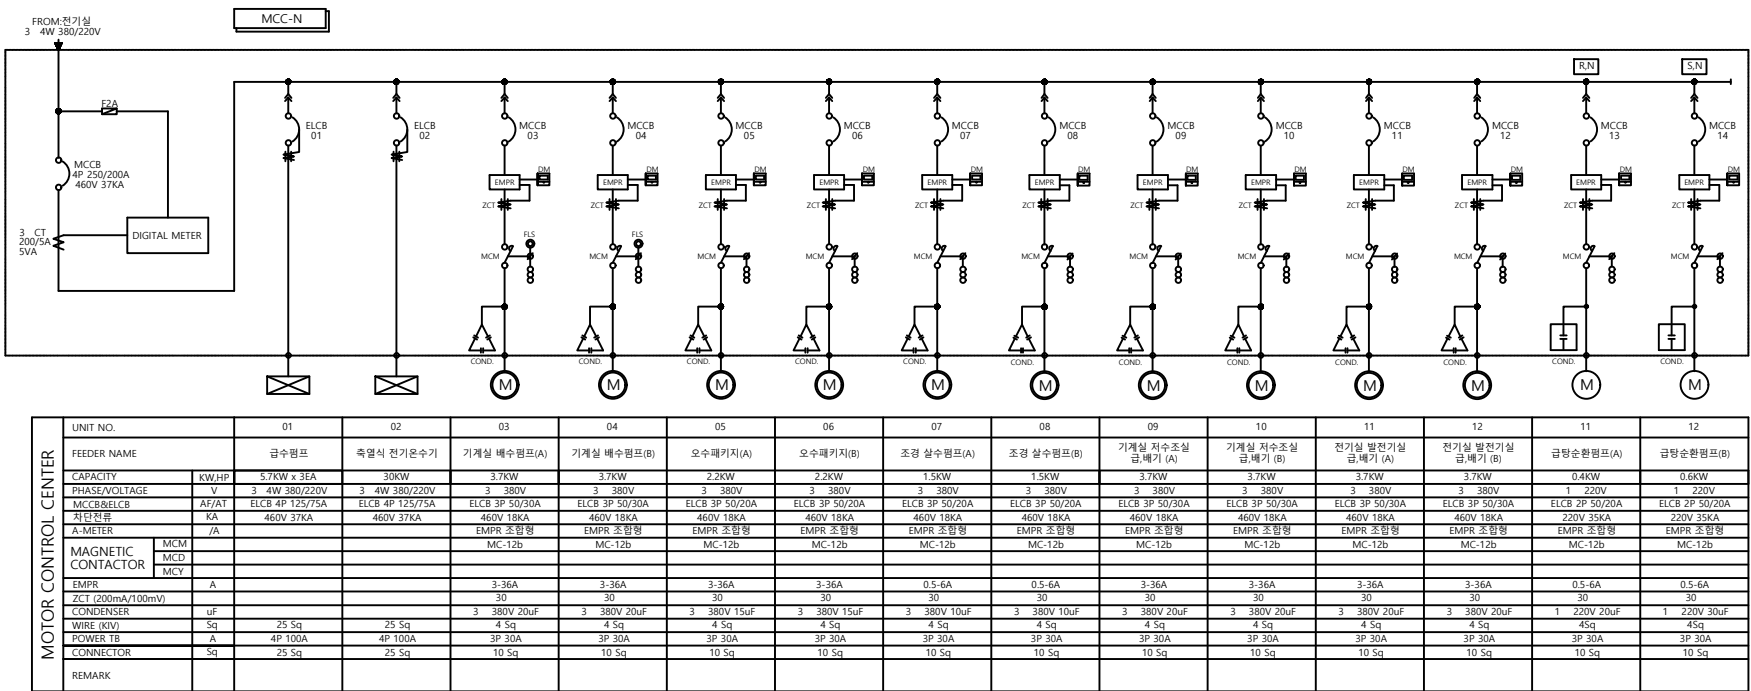

NOTE

- * 보호계전기는 과전류 / 결상 / 단락 / 지락보호 기능이 있는 제품을 사용하고, 보호계전기 1차측 과전류차단기(MCCB)는 지락으로인한 보호계전기 동작시 연동가능한 제품(Short Coil Trip Device내장형)사용을 원칙으로 한다.(소방부하 제외)
- * MCC반은 인출형 임.


1

MCC 결선도


S=A1:1/NONE, A3:1/NONE

(주) 신화엔지니어링 종합건축사사무소
전문설계업 1종 제 1-2-12 호
발송배전기술사 오 정 근 (인)
대전광역시 동구 용전동 143-21번지 TEL:(042) 670-3191~4

N P (320x60)	MCC-N (3 4W 380/220V)			MCC-F (3 4W 380/220V)	
-----------------	--------------------------	--	--	--------------------------	--

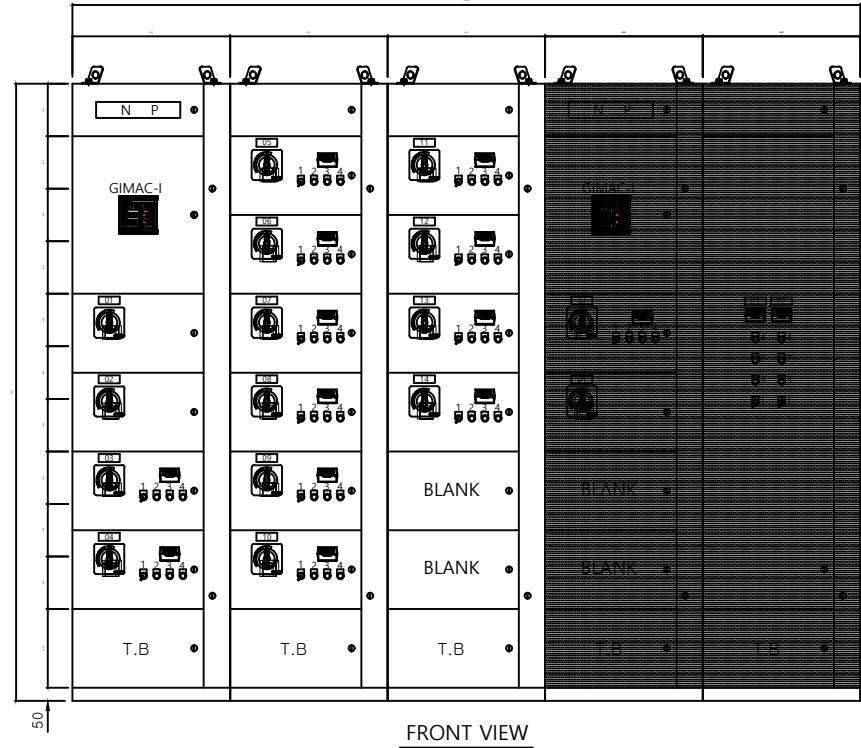

FRONT VIEW

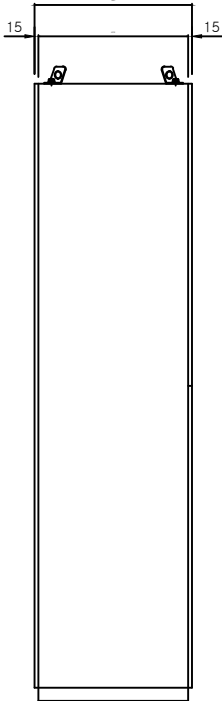

SIDE VIEW

NOTE		
1	구 조	육내 노출자립형
2	FRAME	ANGLELESS TYPE 2.3t
3	UNIT DOOR	STEEL 2.3t
4	REAR DOOR	STEEL 2.3t
5	SIDE	STEEL 2.3t
6	TOP	STEEL 2.3t
7	BOTTOM	STEEL 2.3t
8	COLOR	MUNSELL NO. 5Y 7/1
9		적색도장

	OPERATE HANDLE
	GIMAC-i
	EMPR DISPLAY
	FASTENER
	UNIT NAME PLATE

NO.	품 명	N P	CAP
1	SEL S/W 25mm	MANU - AUTO	
2	PBL 25mm	ON	RED
3	PBL 25mm	OFF	GREEN
4	PBL 25mm	FAULT & RESET	YELLOW

1 MCC 외함상세도
S=A1:1/NONE, A3:1/NONE


(주) 신화엔지니어링 종합건축사사무소
전 문 설 계 업 1 종 제 1 - 2 - 12 호
발송배전기술사 오 정 근 (인)
대전광역시 동구 용전동 143-21번지 TEL:(042) 670-3191~4

NO.	DATE	REV.DESCRPTION	APPR.


DRAWING TITLE
MCC 외함상세도

APPROVED
CHECKED 2
CHECKED 1
DRAWN BY

SCALE		APPROVAL DATE	
A1	A3	2017. 08.	
1 / NONE	1 / NONE		
DRAWING NO.		REV.	
E - 관급 008			

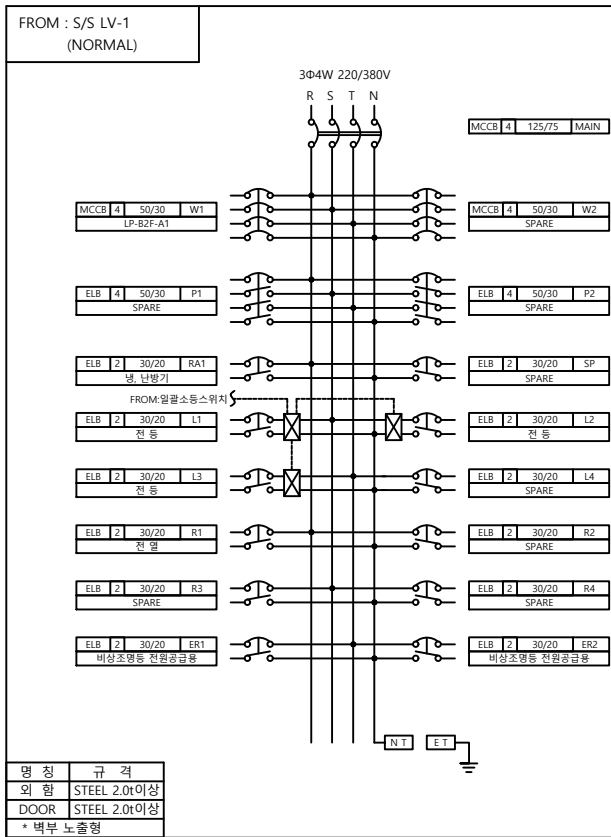


LP-B2F-MA(EPS실)

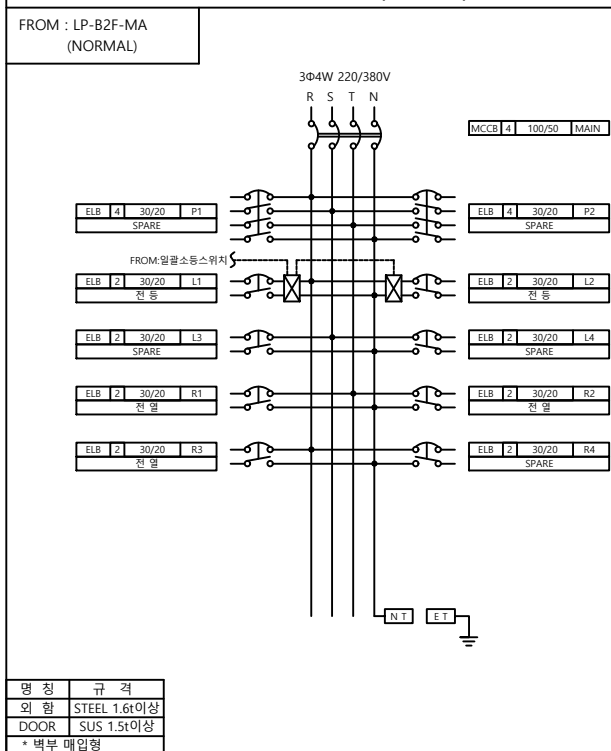


LP-B2F-A1(중앙감시실)

NOTE


- * 차단기는 표준형 이상을 채택할 것.
- * MCCB(MAIN) : 10kA 이상
- * MCCB(BRANCH) : 5kA 이상
- * ELCB : 2.5kA 이상
- * ○ : ELB는 정격감도전류 15mA(고감도형) - 0.03sec(고속형)이내 사용.

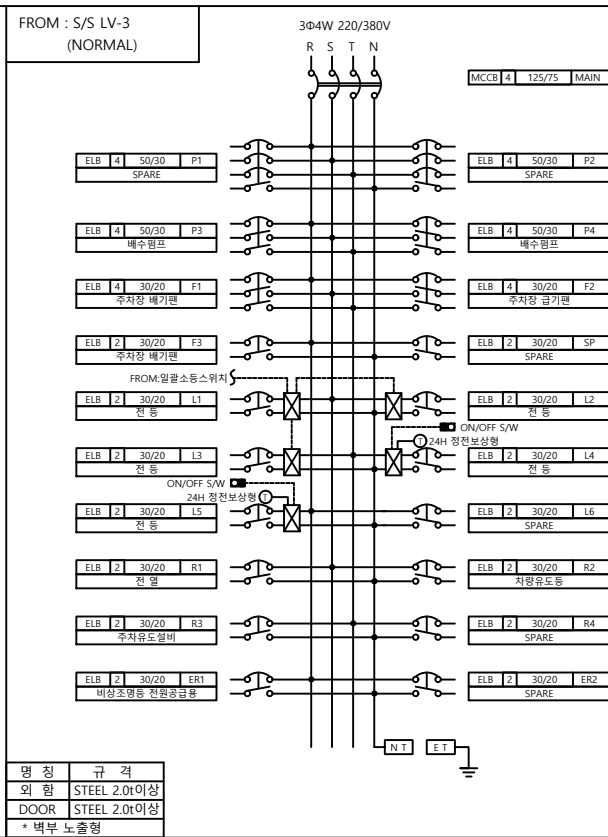


LP-B2F-MB(EPS실)

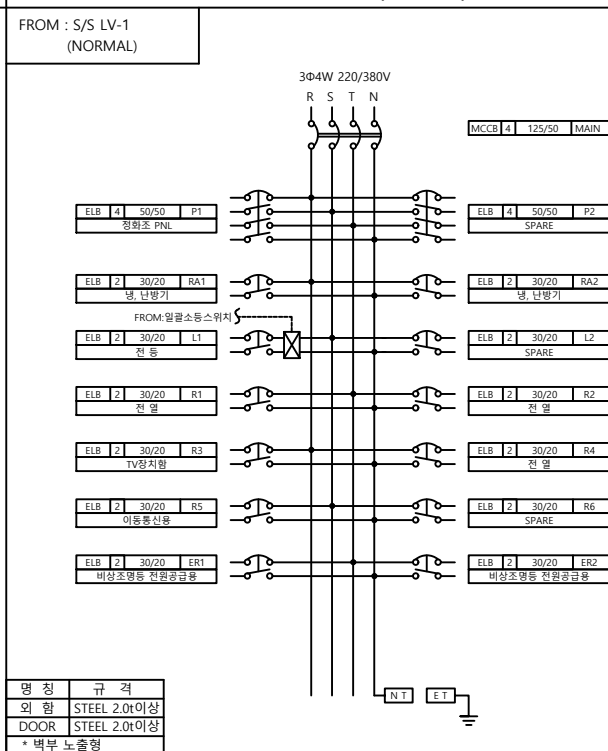

LP-B1F-MA(EPS실)

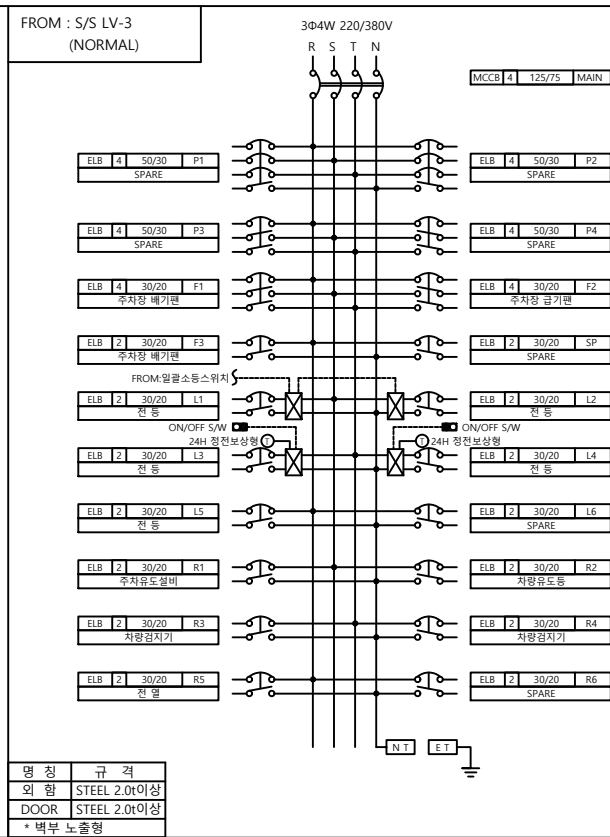

LP-B1F-MB(EPS실)

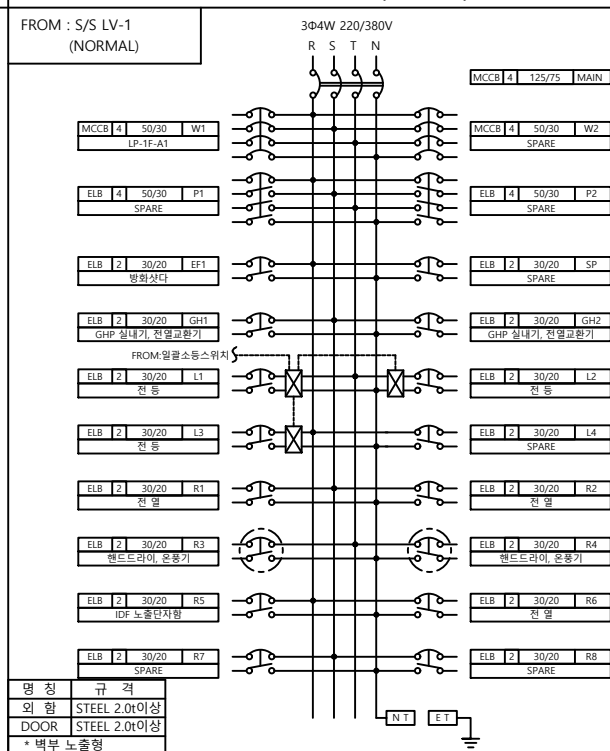

LP-1F-MA(EPS실)

- * 분전반 배면에 결선도를 부착할 수 있는 구조로 제작하여야 한다.
- * 전원표시등은 LED TYPE 으로 설치 할 것.

1 분전반 결선도 (1)
S=A1:1/NONE, A3:1/NONE

(주) 신화엔지니어링 종합건축사사무소
전문설계업 1종 제 1-2-12 호
발송배전기실사 오 정 근 (인)
대전광역시 동구 용전동 143-21번지 TEL:(042) 670-3191~4

PROJECT TITLE

대동지식산업센터
전기공사

DESIGN FIRM

(주) 디엔비건축사사무소

TEL: 042) 823-3724 FAX: 042) 823-9820
Http://WWW.dnbarch.co.kr

SHINHWA
ENGINEERING | ARCHITECTURE

TEL: 042) 670-3175 FAX: 042) 670-3149
Http://WWW.sh-eng.com

NOTE

△			
△			
△			
NO.	DATE	REV. DESCRIPTION	APPR.

DRAWING TITLE

분전반 결선도(1)


APPROVED

CHECKED 2


CHECKED 1

DRAWN BY

SCALE		APPROVAL DATE	
A1	A3		
1 / NONE		2017. 08.	
DRAWING NO.		REV.	
E - 관급 009			

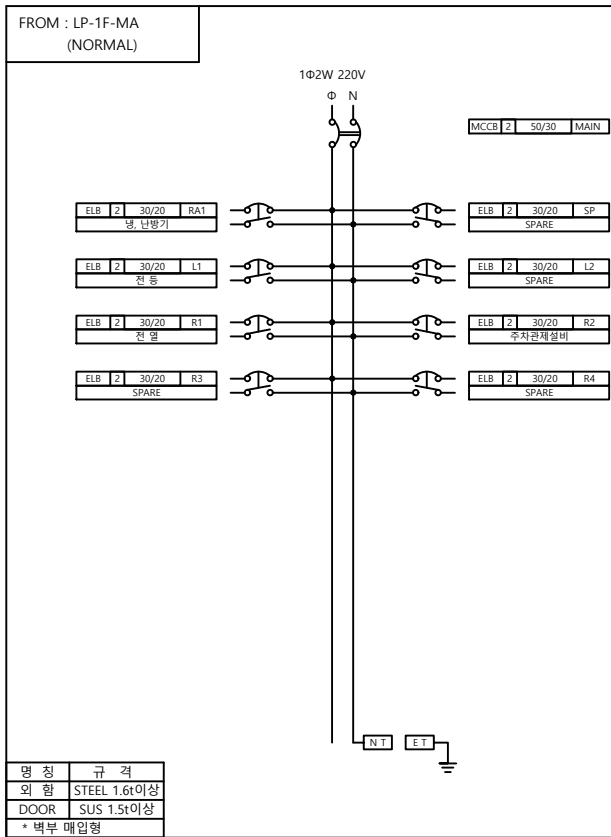


LP-1F-A1(관리실)

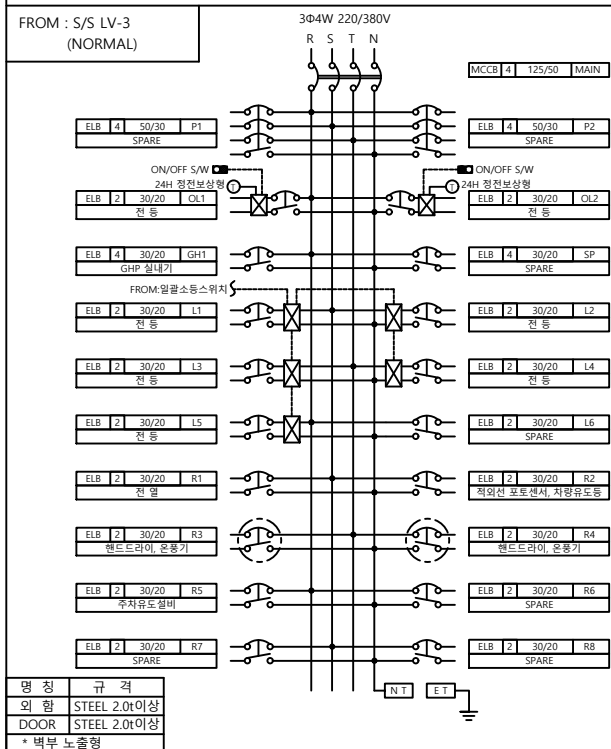


LP-1F-MB(EPS실)

NOTE


* 차단기는 표준형 이상을 채택할 것.
 * MCCB(MAIN) : 10kA 이상
 * MCCB(BRANCH) : 5kA 이상
 * ELCB : 2.5kA 이상
 * ○ : ELB는 정격감도전류 15mA(고감도형) - 0.03sec(고속형)이내 사용.

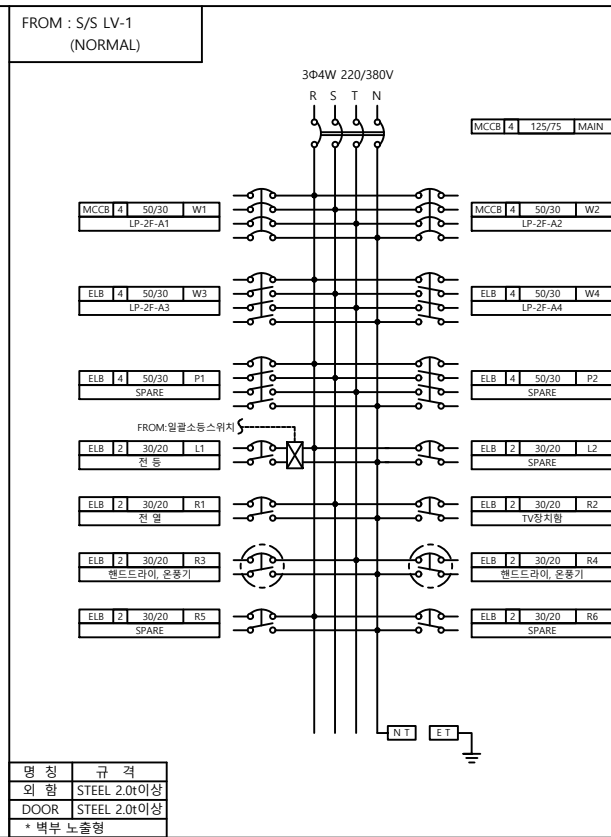


LP-2F-MA(EPS실)

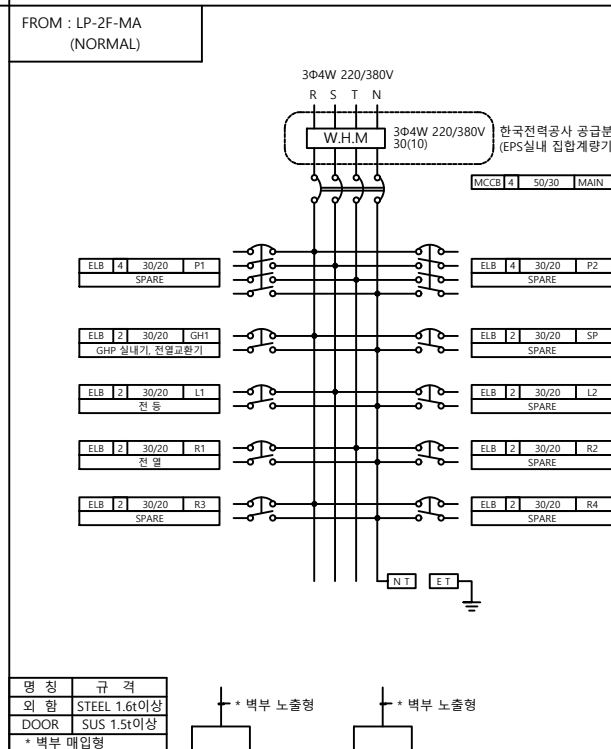

LP-2F-A1, A2, A3, A4(근생1, 2, 3, 4)

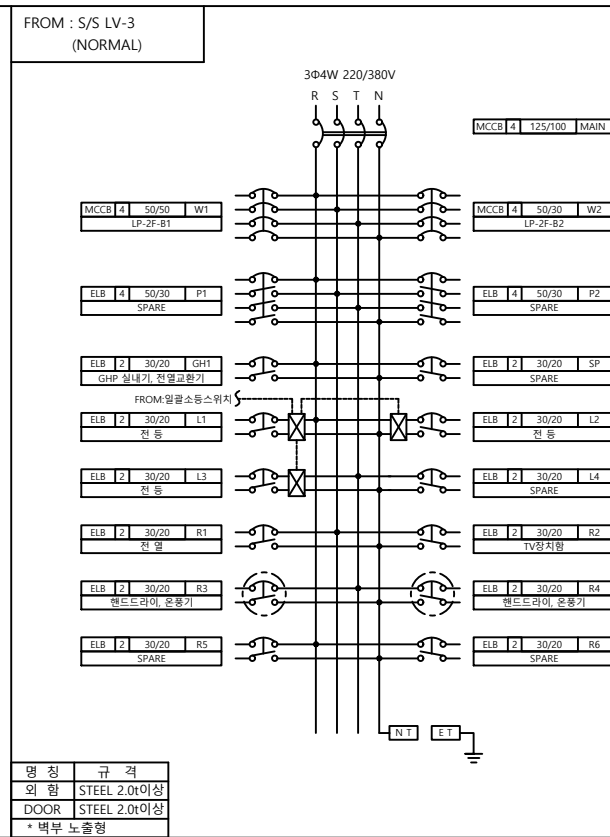

LP-2F-MB(EPS실)

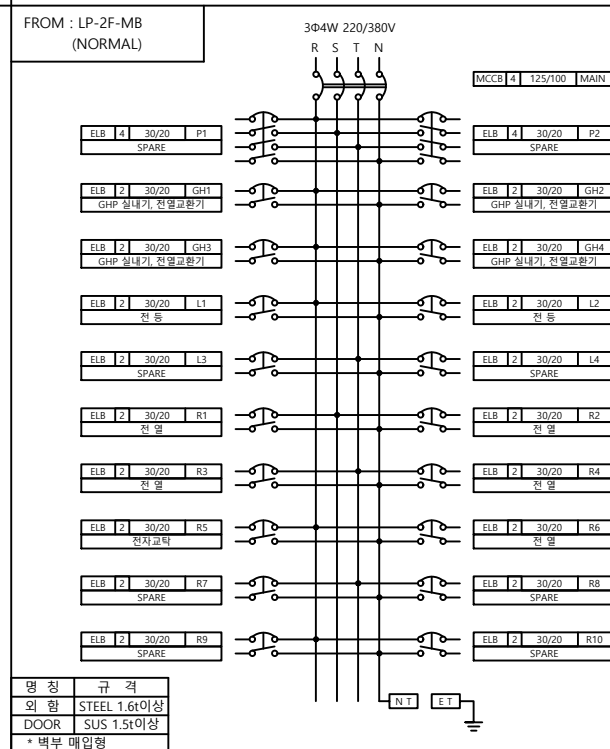

LP-2F-B1(종합사무실)

* 분전반 배면에 결선도를 부착할 수 있는 구조로 제작하여야 한다.
 * 전원표시등은 LED TYPE 으로 설치 할 것.

1 분전반 결선도 (2)
 S=A1:1/NONE, A3:1/NONE

(주) 신화엔지니어링 종합건축사사무소
 전 문 설 계 업 1 종 제 1-2-12 호
 발송배전기술사 오 정 근 (인)
 대전광역시 동구 용전동 143-21번지 TEL:(042) 670-3191~4

DCCO 대전도시공사

PROJECT TITLE
 대동지식산업센터 전기공사

DESIGN FIRM
 (주) 디엔비건축사사무소
 TEL: 042) 823-3724 FAX: 042) 823-9820
 Http://WWW.dnbarch.co.kr

SHINHWA ENGINEERING | ARCHITECTURE
 TEL: 042) 670-3175 FAX: 042) 670-3149
 Http://WWW.sh-eng.com

NOTE

△			
△			
△			
NO.	DATE	REV.DESRIPTION	APPR.



DRAWING TITLE
 분전반 결선도(2)

APPROVED
 CHECKED 2
 CHECKED 1
 DRAWN BY

SCALE
 A1 A3
 1 / NONE 1 / NONE



APPROVAL DATE
 2017. 08.

DRAWING NO.
 E - 관급 010

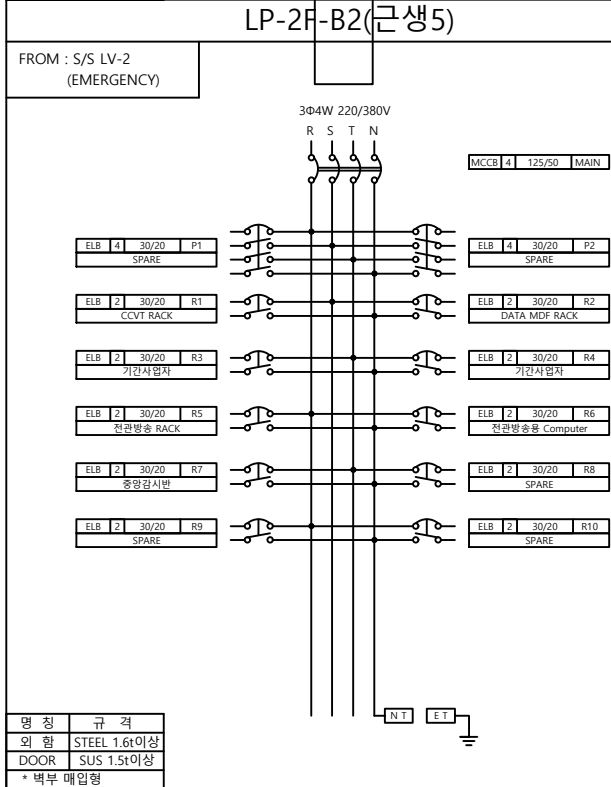
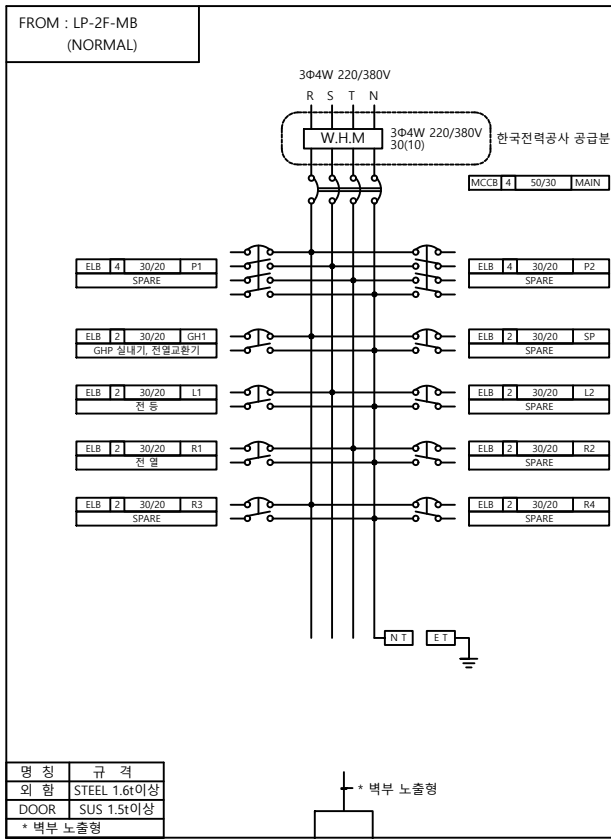


NOTE

* 차단기는 표준형 이상을 채택할 것.
* MCCB(MAIN) : 10kA 이상
* MCCB(BRANCH) : 5kA 이상
* ELCB : 2.5kA 이상
* (○) : ELB는 정전감도전류 15mA(고감도형) - 0.03sec(고속형)이내 사용.

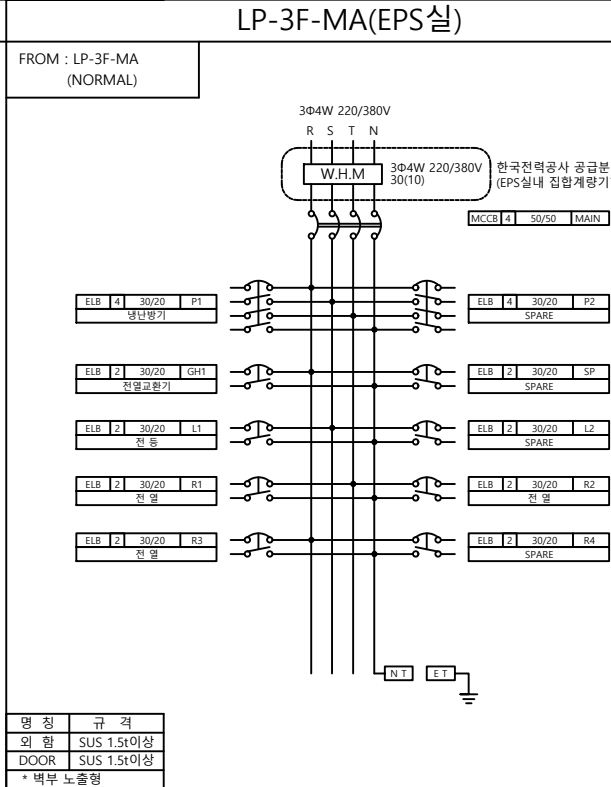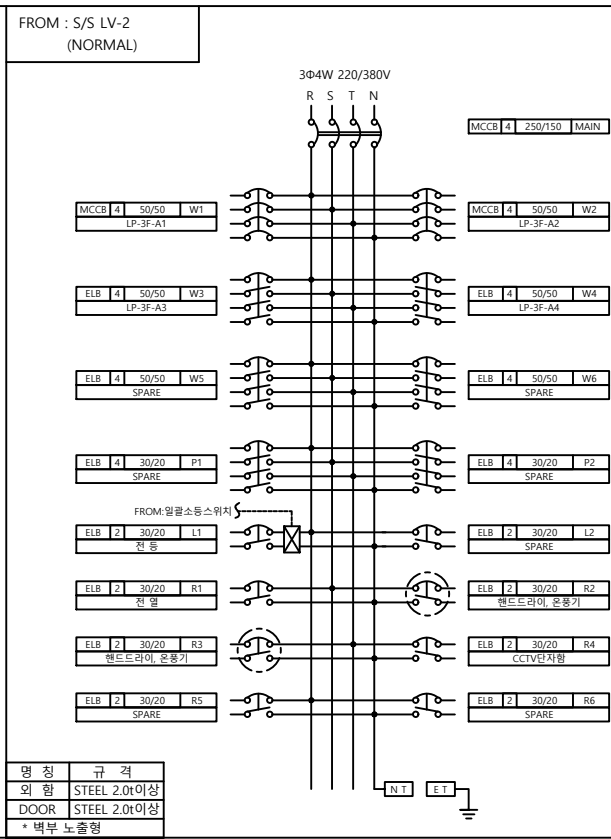

분전반 결선도 (3)
S=A1:1/NONE, A3:1/NONE

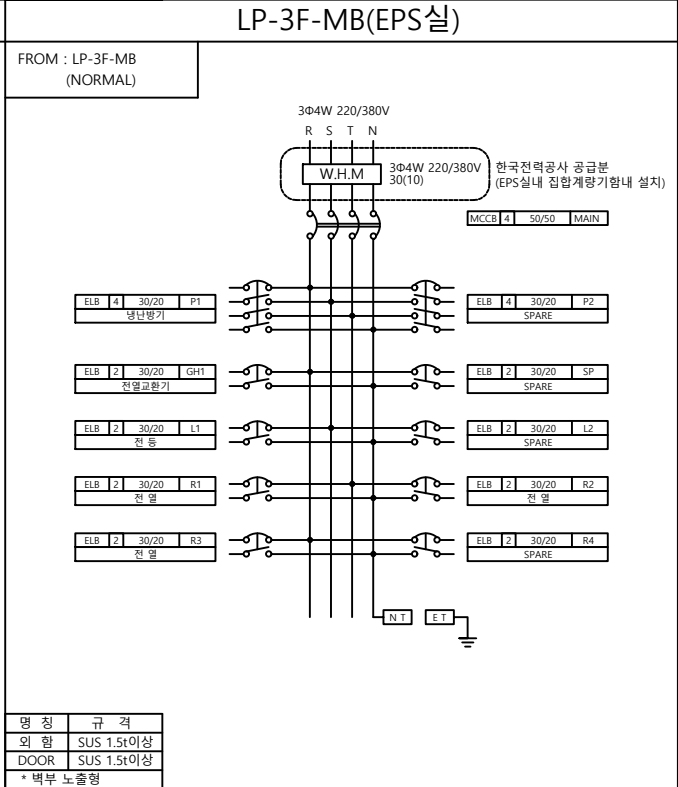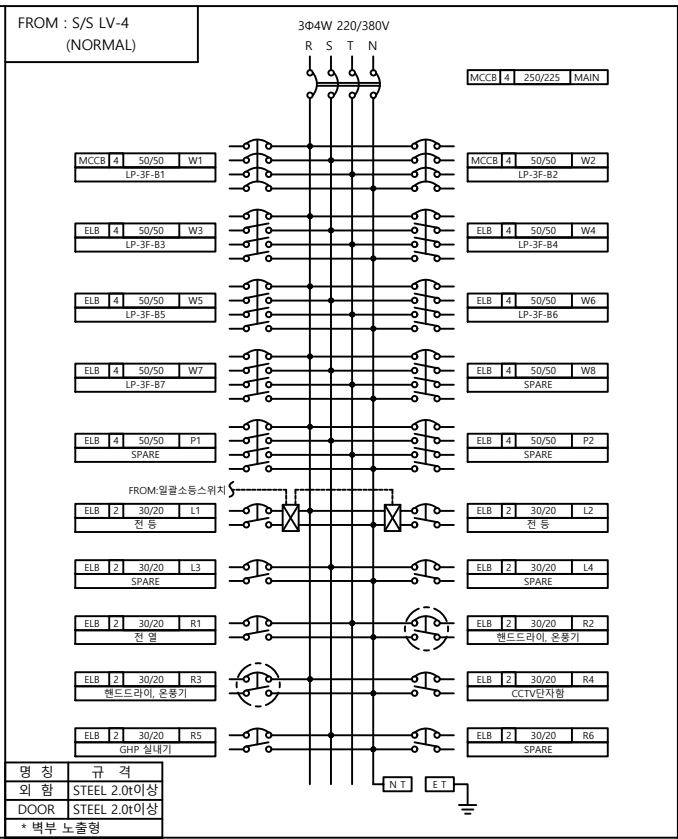

분전반 결선도 (3)

* 분전반 배면에 결선도를 부착할 수 있는 구조로 제작하여야 한다.
* 전원표시등은 LED TYPE 으로 설치 할 것.

(주) 신화엔지니어링 종합건축사사무소
전 문 설 계 업 1 종 제 1-2-12 호
발송배전기술사 오 정 근 (인)
대전광역시 동구 용전동 143-21번지 TEL:(042) 670-3191~4



PROJECT TITLE
대동지식산업센터
전기공사

DESIGN FIRM
(주) 디엔비건축사사무소
TEL: 042) 823-3724 FAX: 042) 823-9820
Http://WWW.dnbarch.co.kr

SHINHWA
ENGINEERING | ARCHITECTURE
TEL: 042) 670-3175 FAX: 042) 670-3149
Http://WWW.sh-eng.com


NOTE

△			
△			
△			
NO.	DATE	REV.DESRIPTION	APPR.


DRAWING TITLE
분전반 결선도(3)

APPROVED
CHECKED 2
CHECKED 1
DRAWN BY

SCALE	APPROVAL DATE
A1	A3
1 / NONE	1 / NONE
DRAWING NO.	REV.
E -	관급 011

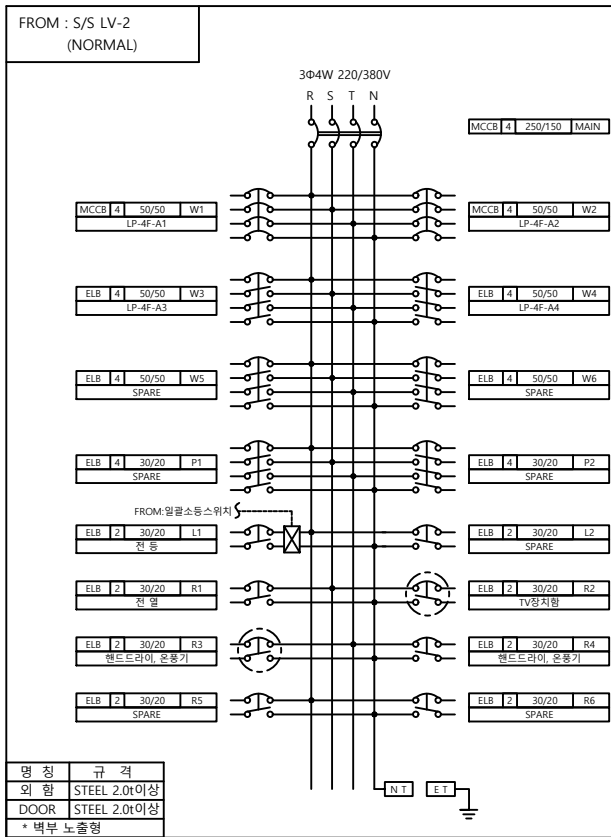


LP-4F-MA(EPS실)

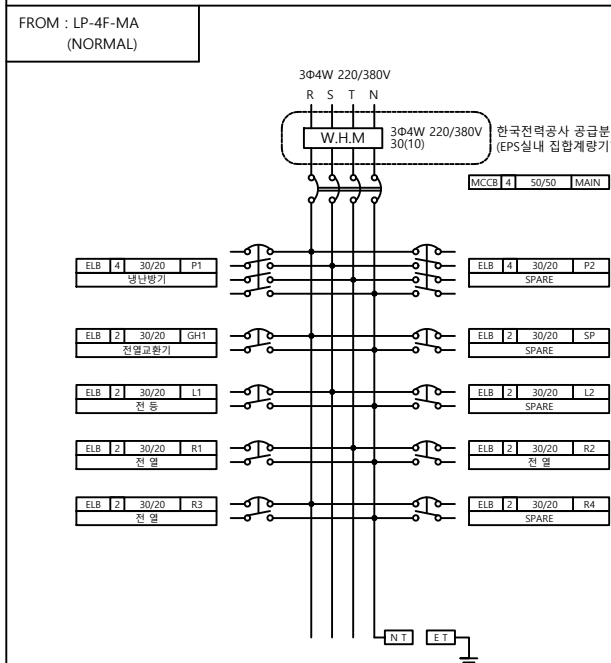


LP-4F-A1~A4(401, 402, 404, 405호)

NOTE


- * 차단기는 표준형 이상을 채택할 것.
- * MCCB(MAIN) : 10kA 이상
- * MCCB(BRANCH) : 5kA 이상
- * ELCB : 2.5kA 이상
- * (○) : ELB는 정격감도전류 15mA(고감도형) - 0.03sec(고속형)이내 사용.

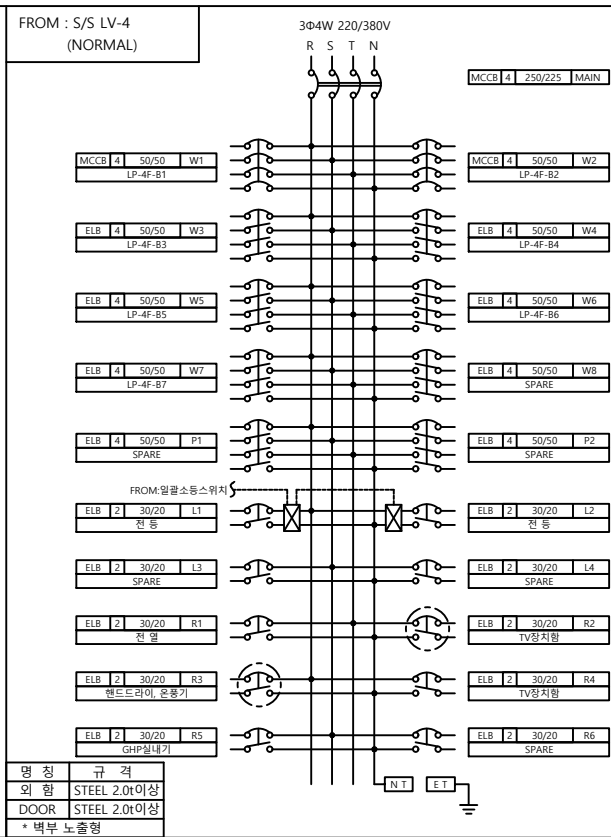


LP-4F-MB(EPS실)

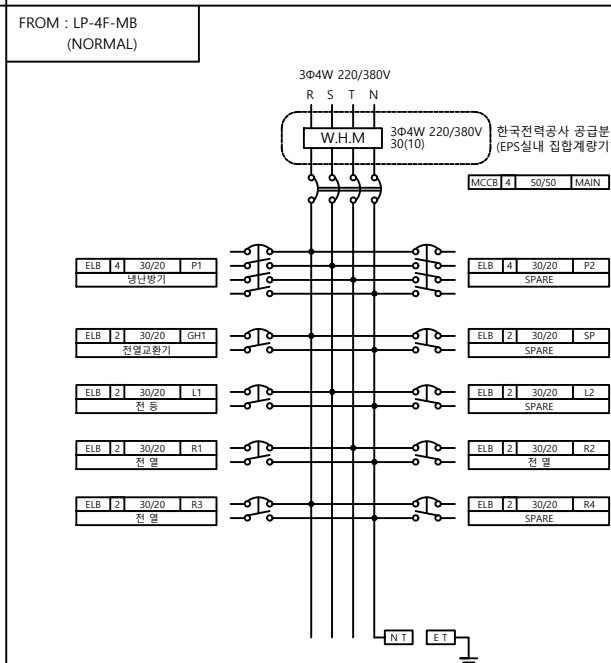

LP-4F-B1~B7(406~412호)

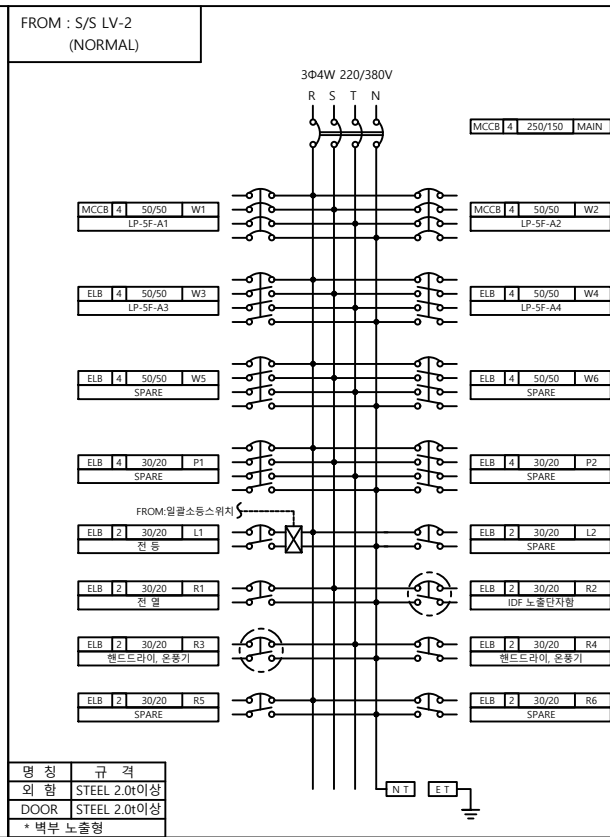

LP-5F-MA(EPS실)

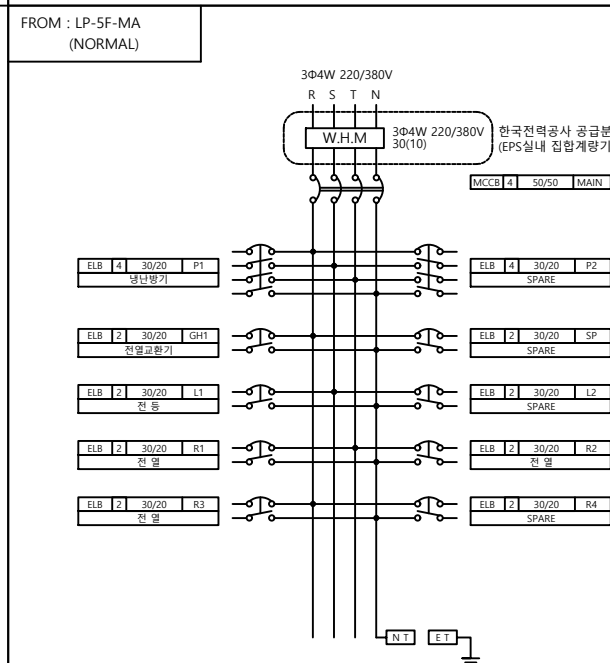

LP-5F-A1~A4(501, 502, 504, 505호)

- * 본전반 배면에 결선도를 부착할 수 있는 구조로 제작하여야 한다.
- * 전원표시등은 LED TYPE 으로 설치 할 것.

1 본전반 결선도 (4)
S=A1:1/NONE, A3:1/NONE

(주) 신화엔지니어링 종합건축사사무소
전 문 설 계 업 1 종 제 1-2-12 호
발송배전기술사 오 정 근 (인)
대전광역시 동구 용전동 143-21번지 TEL:(042) 670-3191~4

DCCO 대전도시공사

PROJECT TITLE
대동지식산업센터 전기공사

DESIGN FIRM
(주) 디엔비건축사사무소
TEL: 042) 823-3724 FAX: 042) 823-9820
Http://WWW.dnbarch.co.kr

SHINHWA ENGINEERING | ARCHITECTURE
TEL: 042) 670-3175 FAX: 042) 670-3149
Http://WWW.sh-eng.com

NOTE

△			
△			
△			
NO.	DATE	REV.DESRIPTION	APPR.


DRAWING TITLE
본전반 결선도(4)

APPROVED
CHECKED 2
CHECKED 1
DRAWN BY


SCALE
A1 A3
1/NONE 1/NONE

APPROVAL DATE
2017. 08.


DRAWING NO.
E - 관급 012

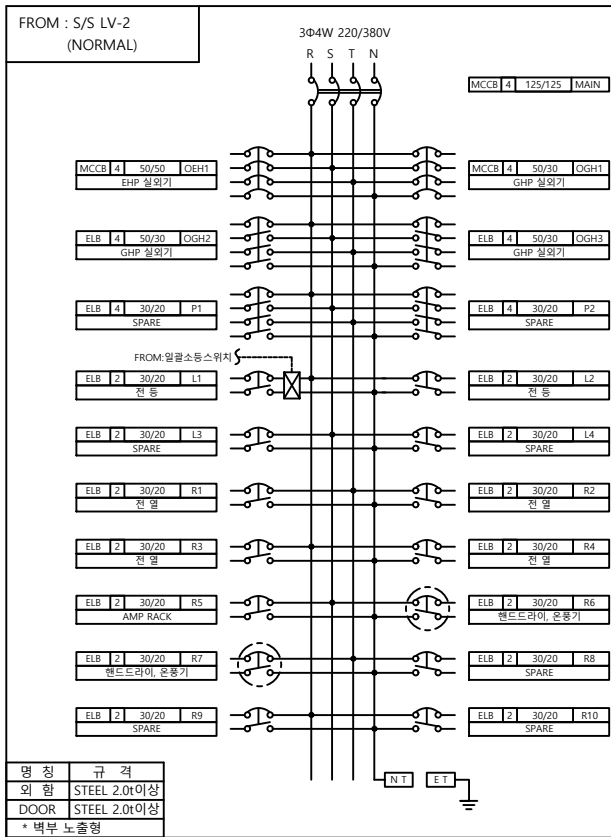


LP-7F-MA(EPS실)

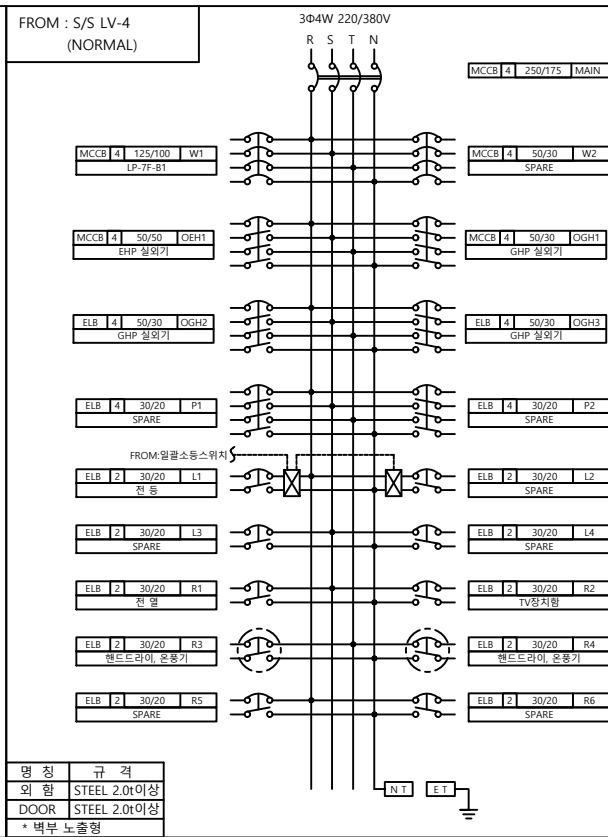


LP-7F-MB(EPS실)

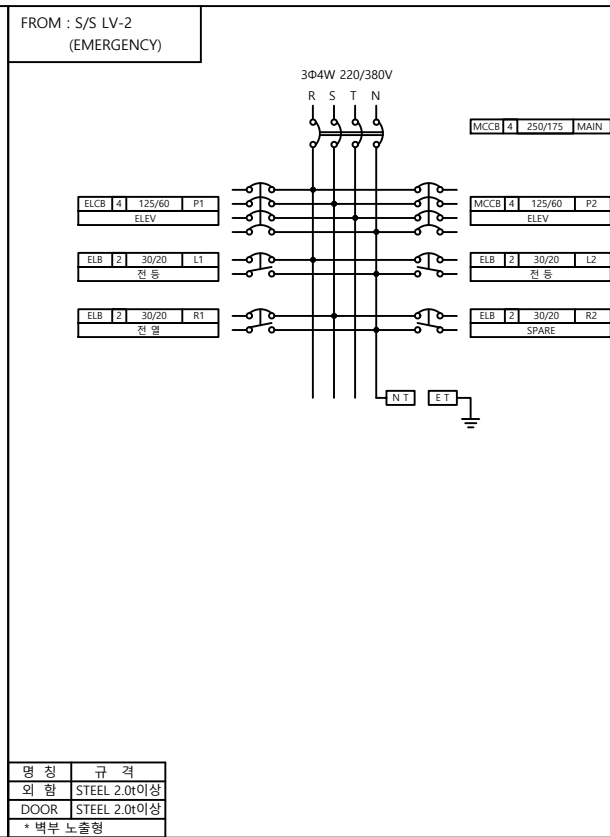

P-ELEV (1), (3)-2면

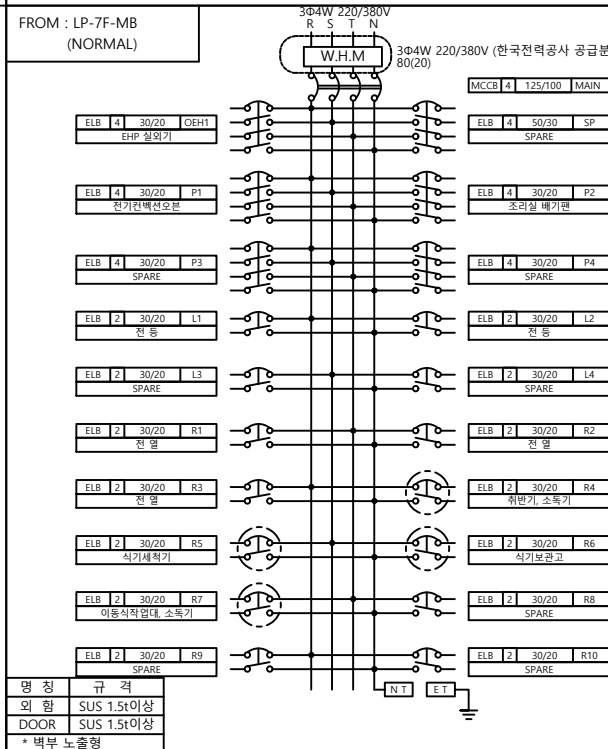

LP-7F-B1(주방)

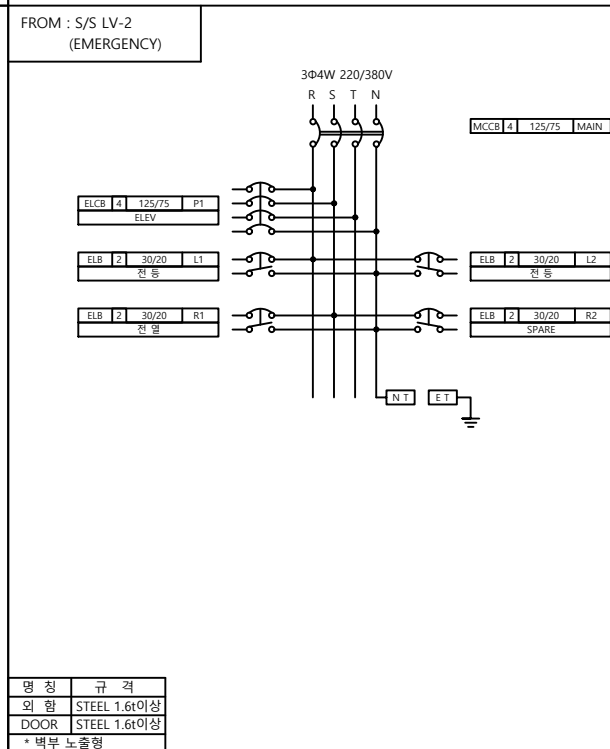

P-ELEV (2)

NOTE

- * 차단기는 표준형 이상을 채택할 것.
- * MCCB(MAIN) : 10kA 이상
- * MCCB(BRANCH) : 5kA 이상
- * ELCB : 2.5kA 이상
- * ○: ELB는 정격감도전류 15mA(고감도형) - 0.03sec(고속형)이내 사용.

1 분전반 결선도 (6)
S=A1:1/NONE, A3:1/NONE

- * 분전반 배면에 결선도를 부착할 수 있는 구조로 제작하여야 한다.
- * 전원표시등은 LED TYPE 으로 설치 할 것.

(주) 신화엔지니어링 종합건축사사무소
전 문 설 계 업 1 종 제 1 - 2 - 12 호
발송배전기술사 오 정 근 (인)
대전광역시 동구 용전동 143-21번지 TEL:(042) 670-3191~4

DCCO 대전도시공사

PROJECT TITLE
대동지식산업센터 전기공사

DESIGN FIRM
(주) 디엔비건축사사무소
TEL: 042) 823-3724 FAX: 042) 823-9820
Http://WWW.dnbarch.co.kr

SHINHWA
ENGINEERING | ARCHITECTURE
TEL: 042) 670-3175 FAX: 042) 670-3149
Http://WWW.sh-eng.com

NOTE


△			
△			
△			
NO.	DATE	REV.DESCRPTION	APPR.

DRAWING TITLE
분전반 결선도(6)

APPROVED
CHECKED 2
CHECKED 1
DRAWN BY


SCALE	APPROVAL DATE
A1 A3	
1 / NONE 1 / NONE	2017. 08.

DRAWING NO. REV.
E - 관급 014

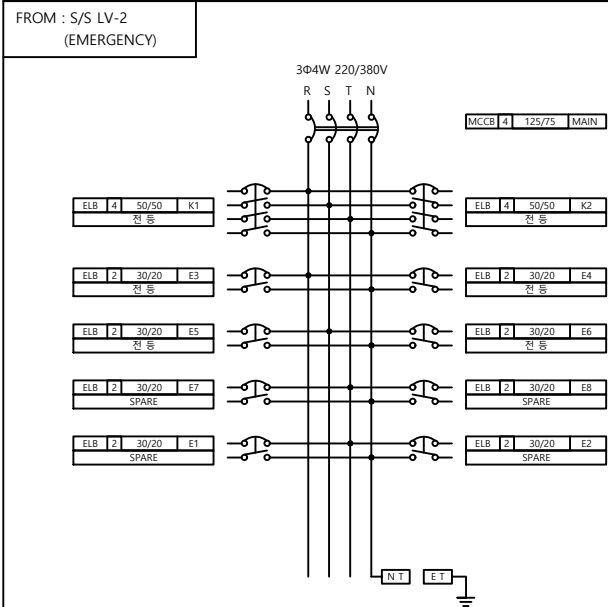

명칭	규격
외함	STEEL 2.0이상
DOOR	STEEL 2.0이상
* 벽부 노출형	

LP-3F-MA(E)(EPS실)

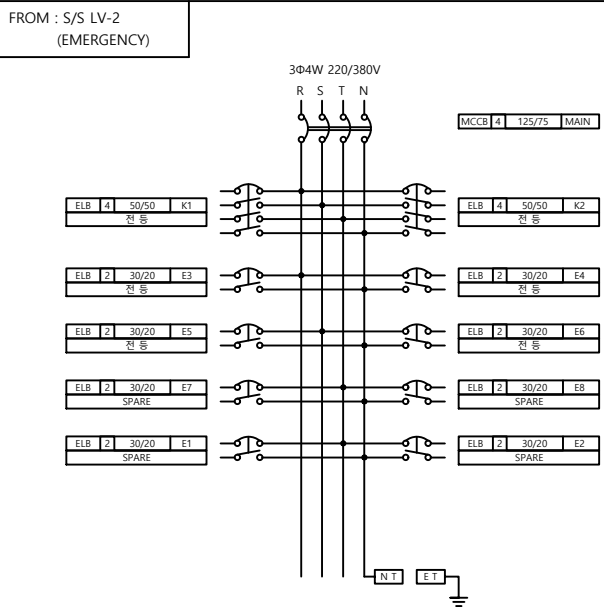

명칭	규격
외함	STEEL 2.0이상
DOOR	STEEL 2.0이상
* 벽부 노출형	

LP-B2F-MB(E)(EPS실)

NOTE

- * 차단기는 표준형 이상을 채택할 것.
- * MCCB(MAIN) : 10kA 이상
- * MCCB(BRANCH) : 5kA 이상
- * ELCB : 2.5kA 이상

* : ELB는 정격감도전류 15mA(고감도형) - 0.03sec(고속형)이내 사용.

1 분전반 결선도(7)
S=A1:1/NONE, A3:1/NONE

- * 분전반 배면에 결선도를 부착할 수 있는 구조로 제작하여야 한다.
- * 전원표시등은 LED TYPE 으로 설치 할 것.

(주) 신화엔지니어링 종합건축사사무소
전 문 설 계 업 1 종 제 1 - 2 - 12 호
발송배전기술사 오 정 근 (인)
대전광역시 동구 용전동 143-21번지 TEL:(042) 670-3191~4



PROJECT TITLE
대동지식산업센터
전기공사

DESIGN FIRM
 (주) 디엔비건축사사무소
TEL: 042) 823-3724 FAX: 042) 823-9820
Http://WWW.dnbarch.co.kr

SHINHWA
ENGINEERING | ARCHITECTURE
TEL: 042) 670-3175 FAX: 042) 670-3149
Http://WWW.sh-eng.com


NOTE

NO.	DATE	REV.DESCRPTION	APPR.

DRAWING TITLE
분전반 결선도(6)

APPROVED
CHECKED 2
CHECKED 1
DRAWN BY

SCALE		APPROVAL DATE	
A1	A3	2017. 08.	
1 / NONE	1 / NONE		
DRAWING NO.		REV.	
E - 관급		15	

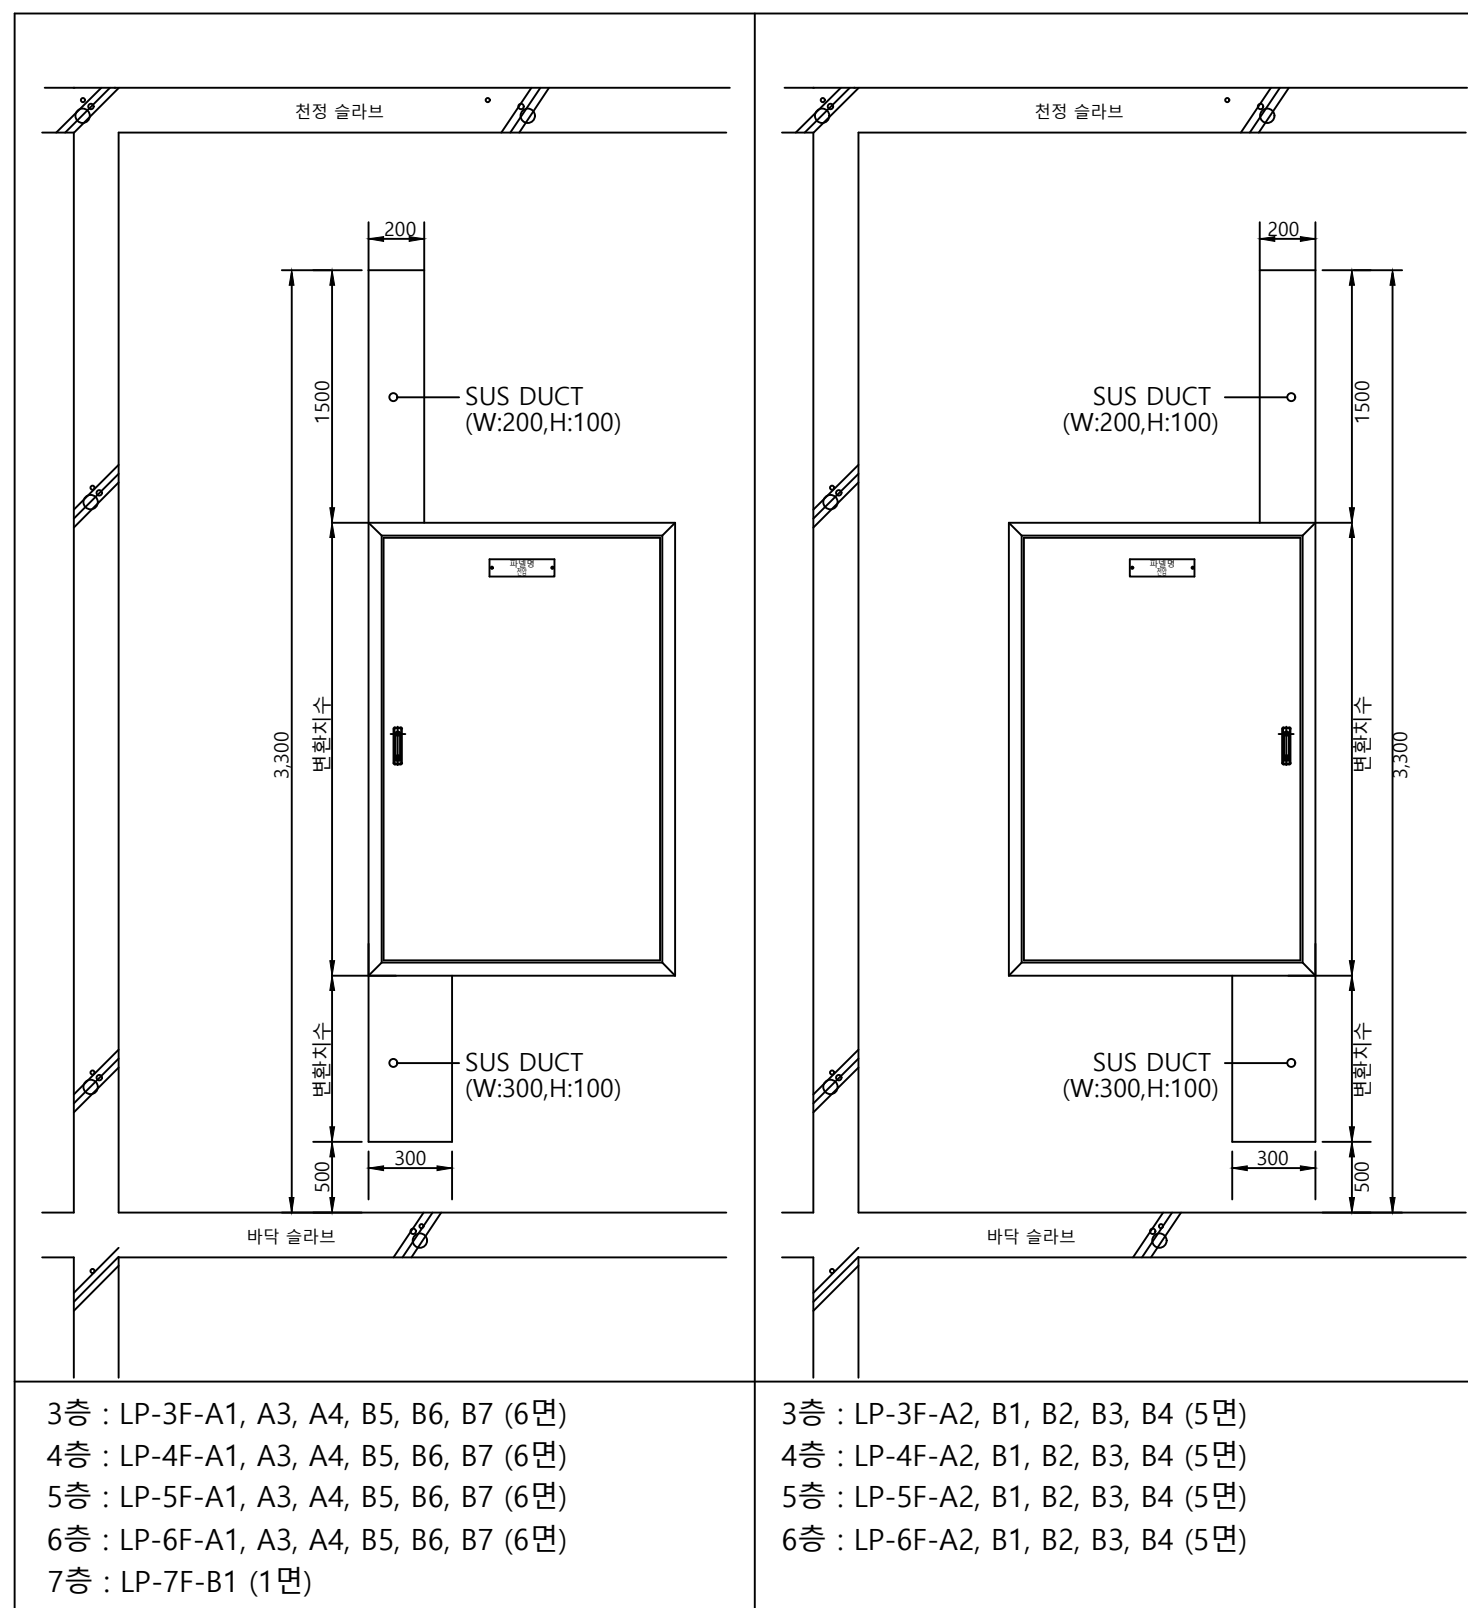

* 관급자재 계약자는 분전반 상,하부 SUS DUCT도 포함해서 납품할 것.

1 분전반 외함(DUCT) 상세도
S=A1:1/NONE, A3:1/NONE

(주) 신화엔지니어링 종합건축사사무소
전 문 설 계 업 1 종 제 1-2-12 호
발송배전기술사 오 정 근 (인)
대전광역시 동구 용전동 143-21번지 TEL:(042) 670-3191~4

△			
△			
△			
NO.	DATE	REV. DESCRIPTION	APPR.
DRAWING TITLE			
분전반 외함(DUCT) 상세도			
APPROVED			
CHECKED 2			
CHECKED 1			
DRAWN BY			
SCALE		APPROVAL DATE	
A1	A3	2017. 08.	
1 / NONE	1 / NONE		
DRAWING NO.		REV.	
E - 관급 016			

